

# Дизайн проект

Будівництво житлового будинку  
с. Віта Поштова, Бучанського р-ну, Київської обл.  
Кадастровий номер: 0000000000:00:000:0000



Київ 2022 р.

## **Відомість робочих креслень.**

## Техніко-економічні показники

Аркуш	Найменування	Примітка
1	Загальні дані	
2	Домокомплект	
3	Схема забудови земельної ділянки М1:200	
4	План фундаменту	
5	План поверху на відмітці 0.000 М1:75	
6	План розташування меблів та сантехніки	
7	План розташування прорізів та їх специфікація	
8	План даху на відмітці +3,600	
9	План даху на відмітці +3,900	
10	План даху на відмітці +5,400	
11	Розріз 1-1, Розріз 2-2	
11	Розріз 3-3. Розріз 4-4	
13	Фасад 1-7, Фасад 7-1 М1:75	
14	Фасад А-К, Фасад К-А М1:75	
15	Вузли	
16	Візуалізація 1	
17	Візуалізація 2	
18	Візуалізація 3	
19	Візуалізація 4	
20	Візуалізація 5	

№	Найменування	Один. виміру	Показники
1	Характер будівництва		Нове будівництво
2	Поверховість будівлі	к-сть	1
3	Висота будівлі	м.	5,7
4	Загальна площа	м.кв.	164,8
5	Площа внутрішніх приміщень	м.кв.	145,5
6	Будівельний об'єм	м.куб.	939,3
	- вище позначки 0.000	м.куб.	889,9
	- нижче позначки 0.000	м.куб.	49,4
7	Площа забудови	м.кв.	164,8
8	Площа забудови з терасами	м.кв.	210,3

					Будівництво індивідуального житлового будинку		
Змін.	Кіл.діл	Аркуш	№ Док.	Підпис	Київська обл., Бучанський р-н, с. Віта Поштова		
			Стадія		Аркуш	Аркушів	
			ЕП		1		
Виконав				Загальні дані			
Перевірив				 <b>УкрСілБуд</b>			

## ДОМОКОМПЛЕКТ СІР ПАНЕЛЕЙ

СТИЛИ:

- Стіни зовнішні СІП 160мм
- Стіни внутрішні СІП 160мм
- Стіни внутрішні СІП 120мм
- Брус стіновий, стартовий 138x60
- Брус з'єднувальний 138x60(30)
- Брус з'єднувальний 98x60(30)

ΔAX:

СІП 200мм  
Брус з'єднувальний 178x60(30)

Каркас Парапету для плоского даху  
СІР 120мм  
Брус з'єднувальний 98x60(30)


## КОМПЛЕКТ КРІПИЛЬНИХ МАТЕРІАЛІВ

Саморізи  
Анкер бетонний  
Бітумний праймер  
Піна монтажна  
Розхідники

Домокомплект СІП панелей комплектується

Пінополістирол ПСБ-С25  
OSB вологостійкий 10мм  
Брус калібрований камерної сушки  
оброблений вогне-біо захистом

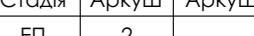



					Будівництво індивідуального житлового будинку			
					Київська обл., Бучанський р-н, с. Віта Поштова	Стадія	Аркуш	Аркушів
Змін.	Кіл.діл	Аркуш	№ Док.	Підпис		ЕП	2	
Виконав					Домокомплект			
Перевірив								



### Умовні позначення:

- дорога
  - вимощення (отмостка)
  - хоз.приміщення
  - навіс
  - дерево
  - кордони ділянки
  - альтанка

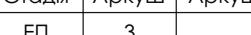					Будівництво індивідуального житлового будинку			
Змін.	Кіл.діл	Аркуш	№ Док.	Підпис	Kиївська обл., Бучанський р-н, с. Віта Поштова	Стадія	Аркуш	Аркушів
						EП	3	
Виконав						Схема забудови земельної ділянки M1:200		
Перевірив						 <b>УКРСІПБУД</b>		

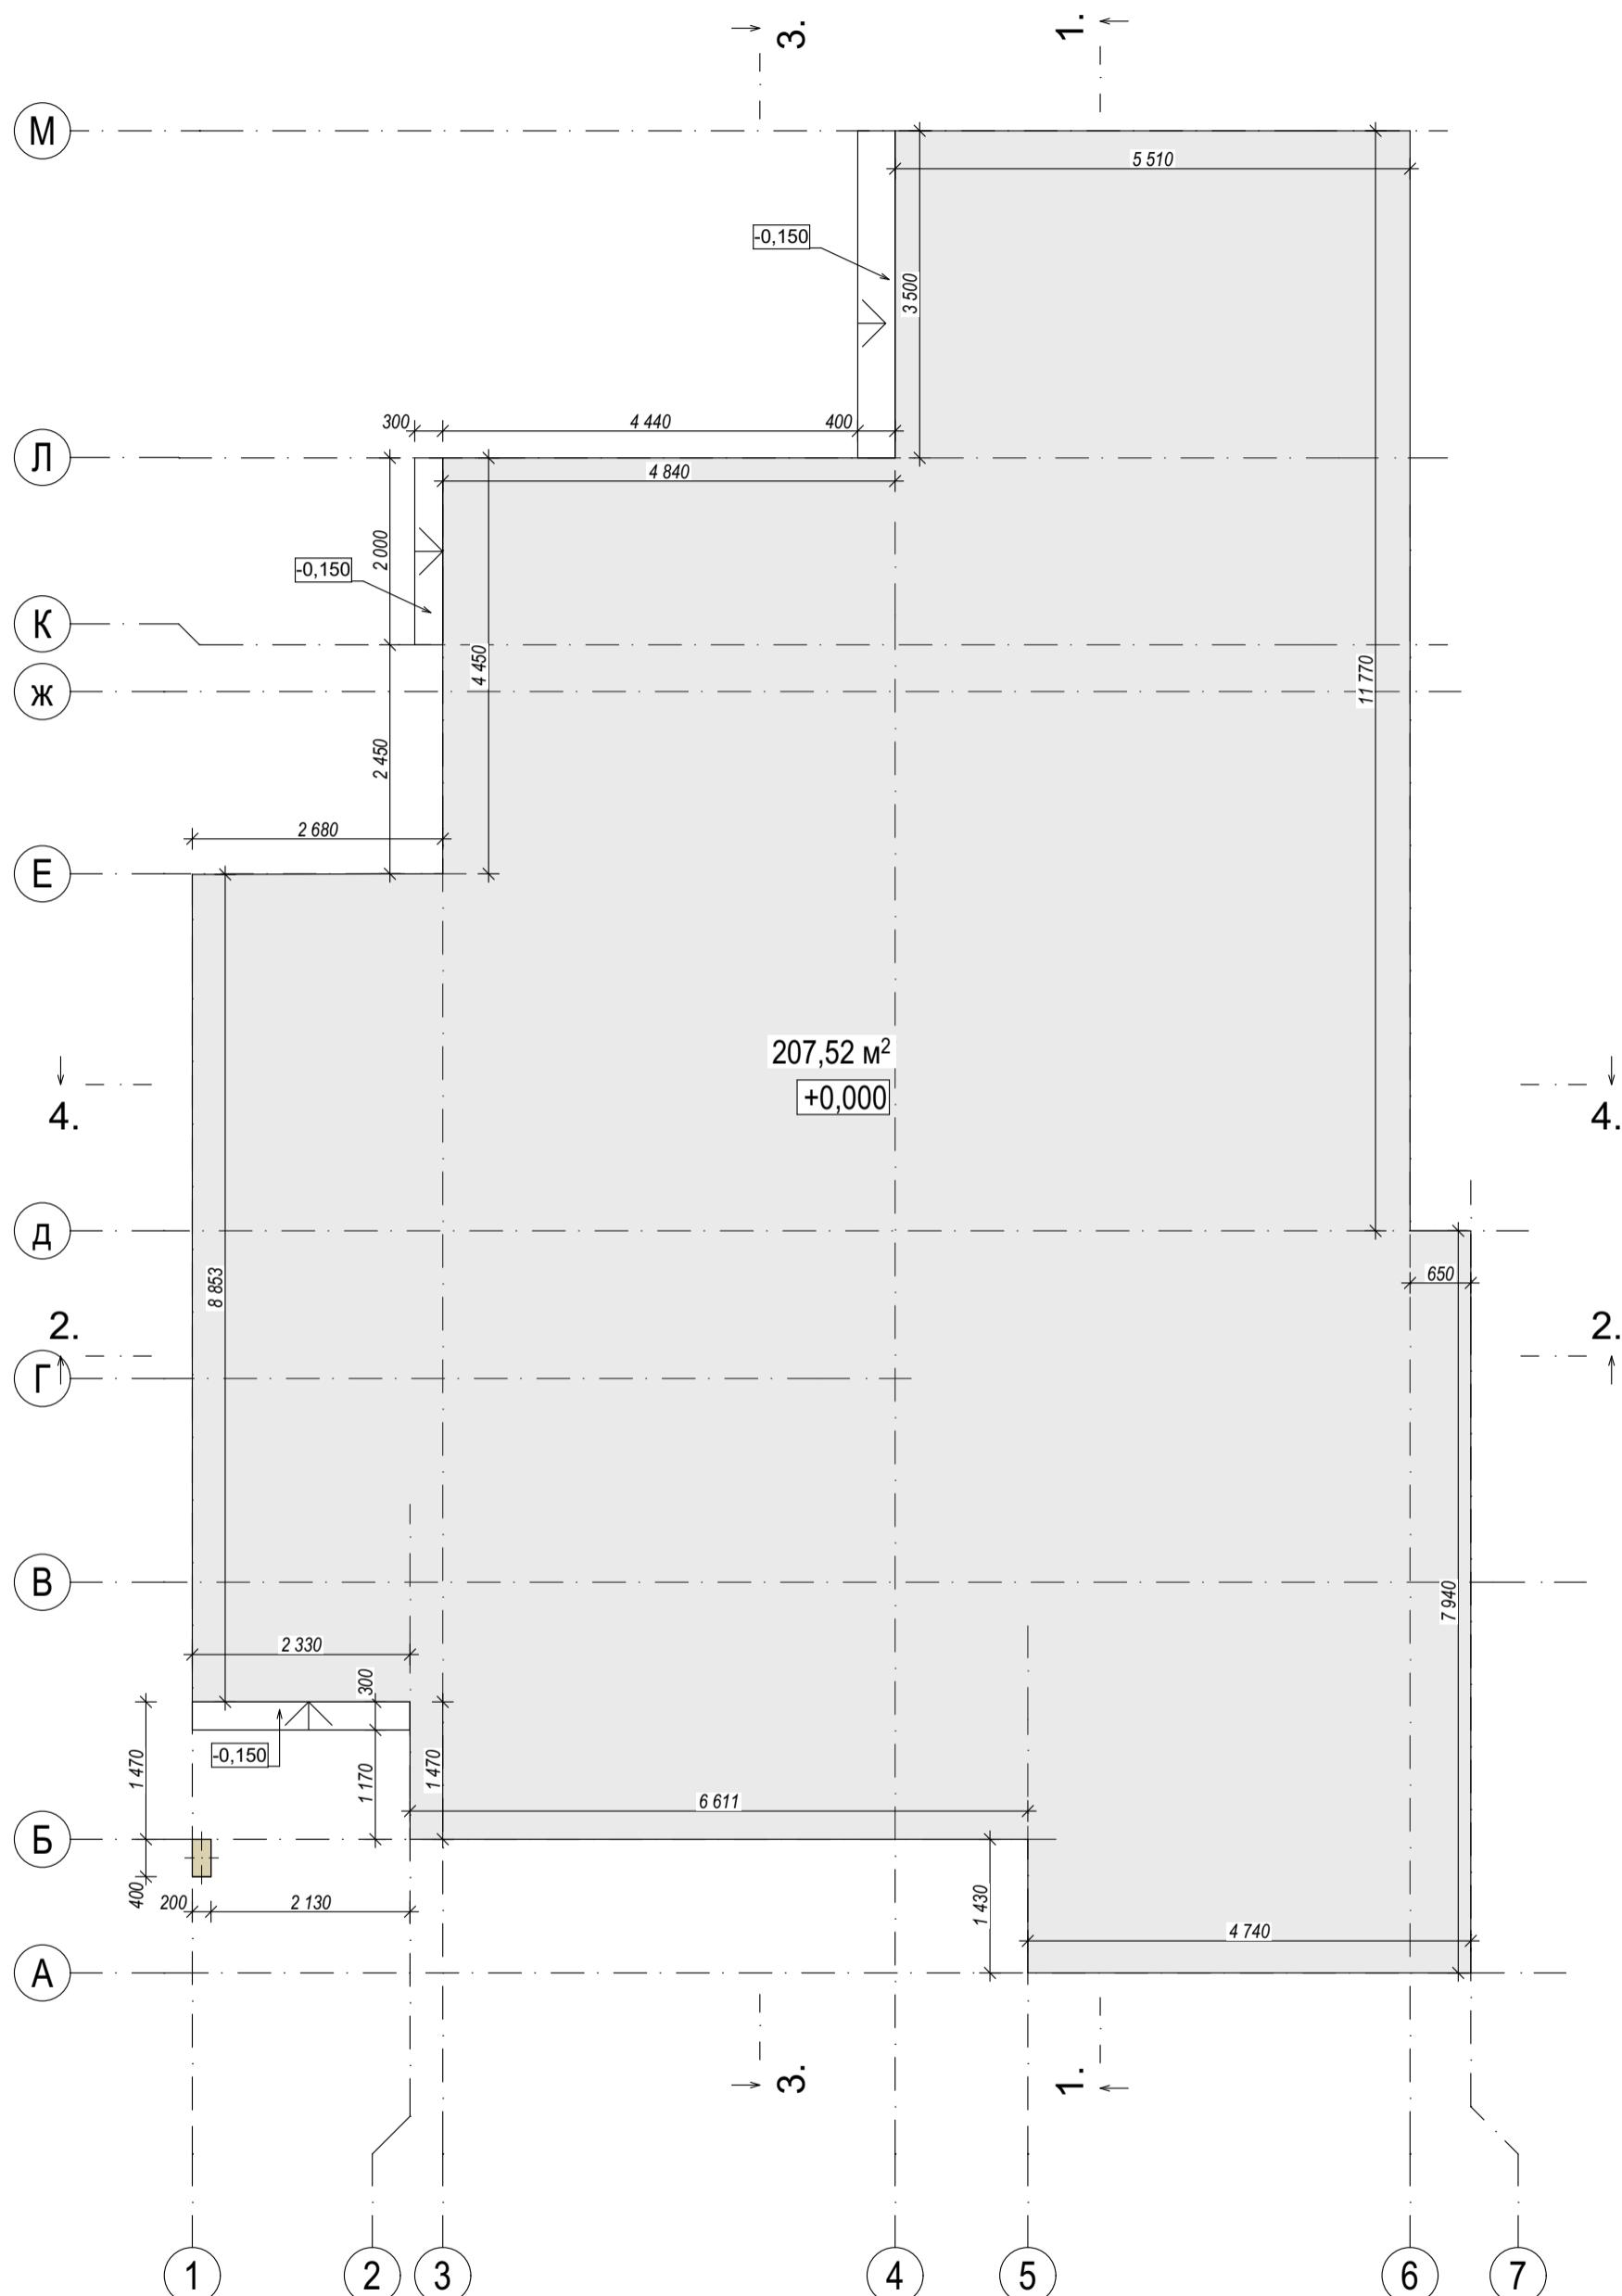


Будівництво індивідуального житлового будинку				
Змін.	Кіл.діл.	Аркуш	№ Док.	Підпис
Виконав				
Перевірив				

Київська обл., Бучанський р-н,  
с. Віта Поштова

Стадія Аркуш Аркушів  
ЕП 4

План фундаменту

**УКРСІПБУД**

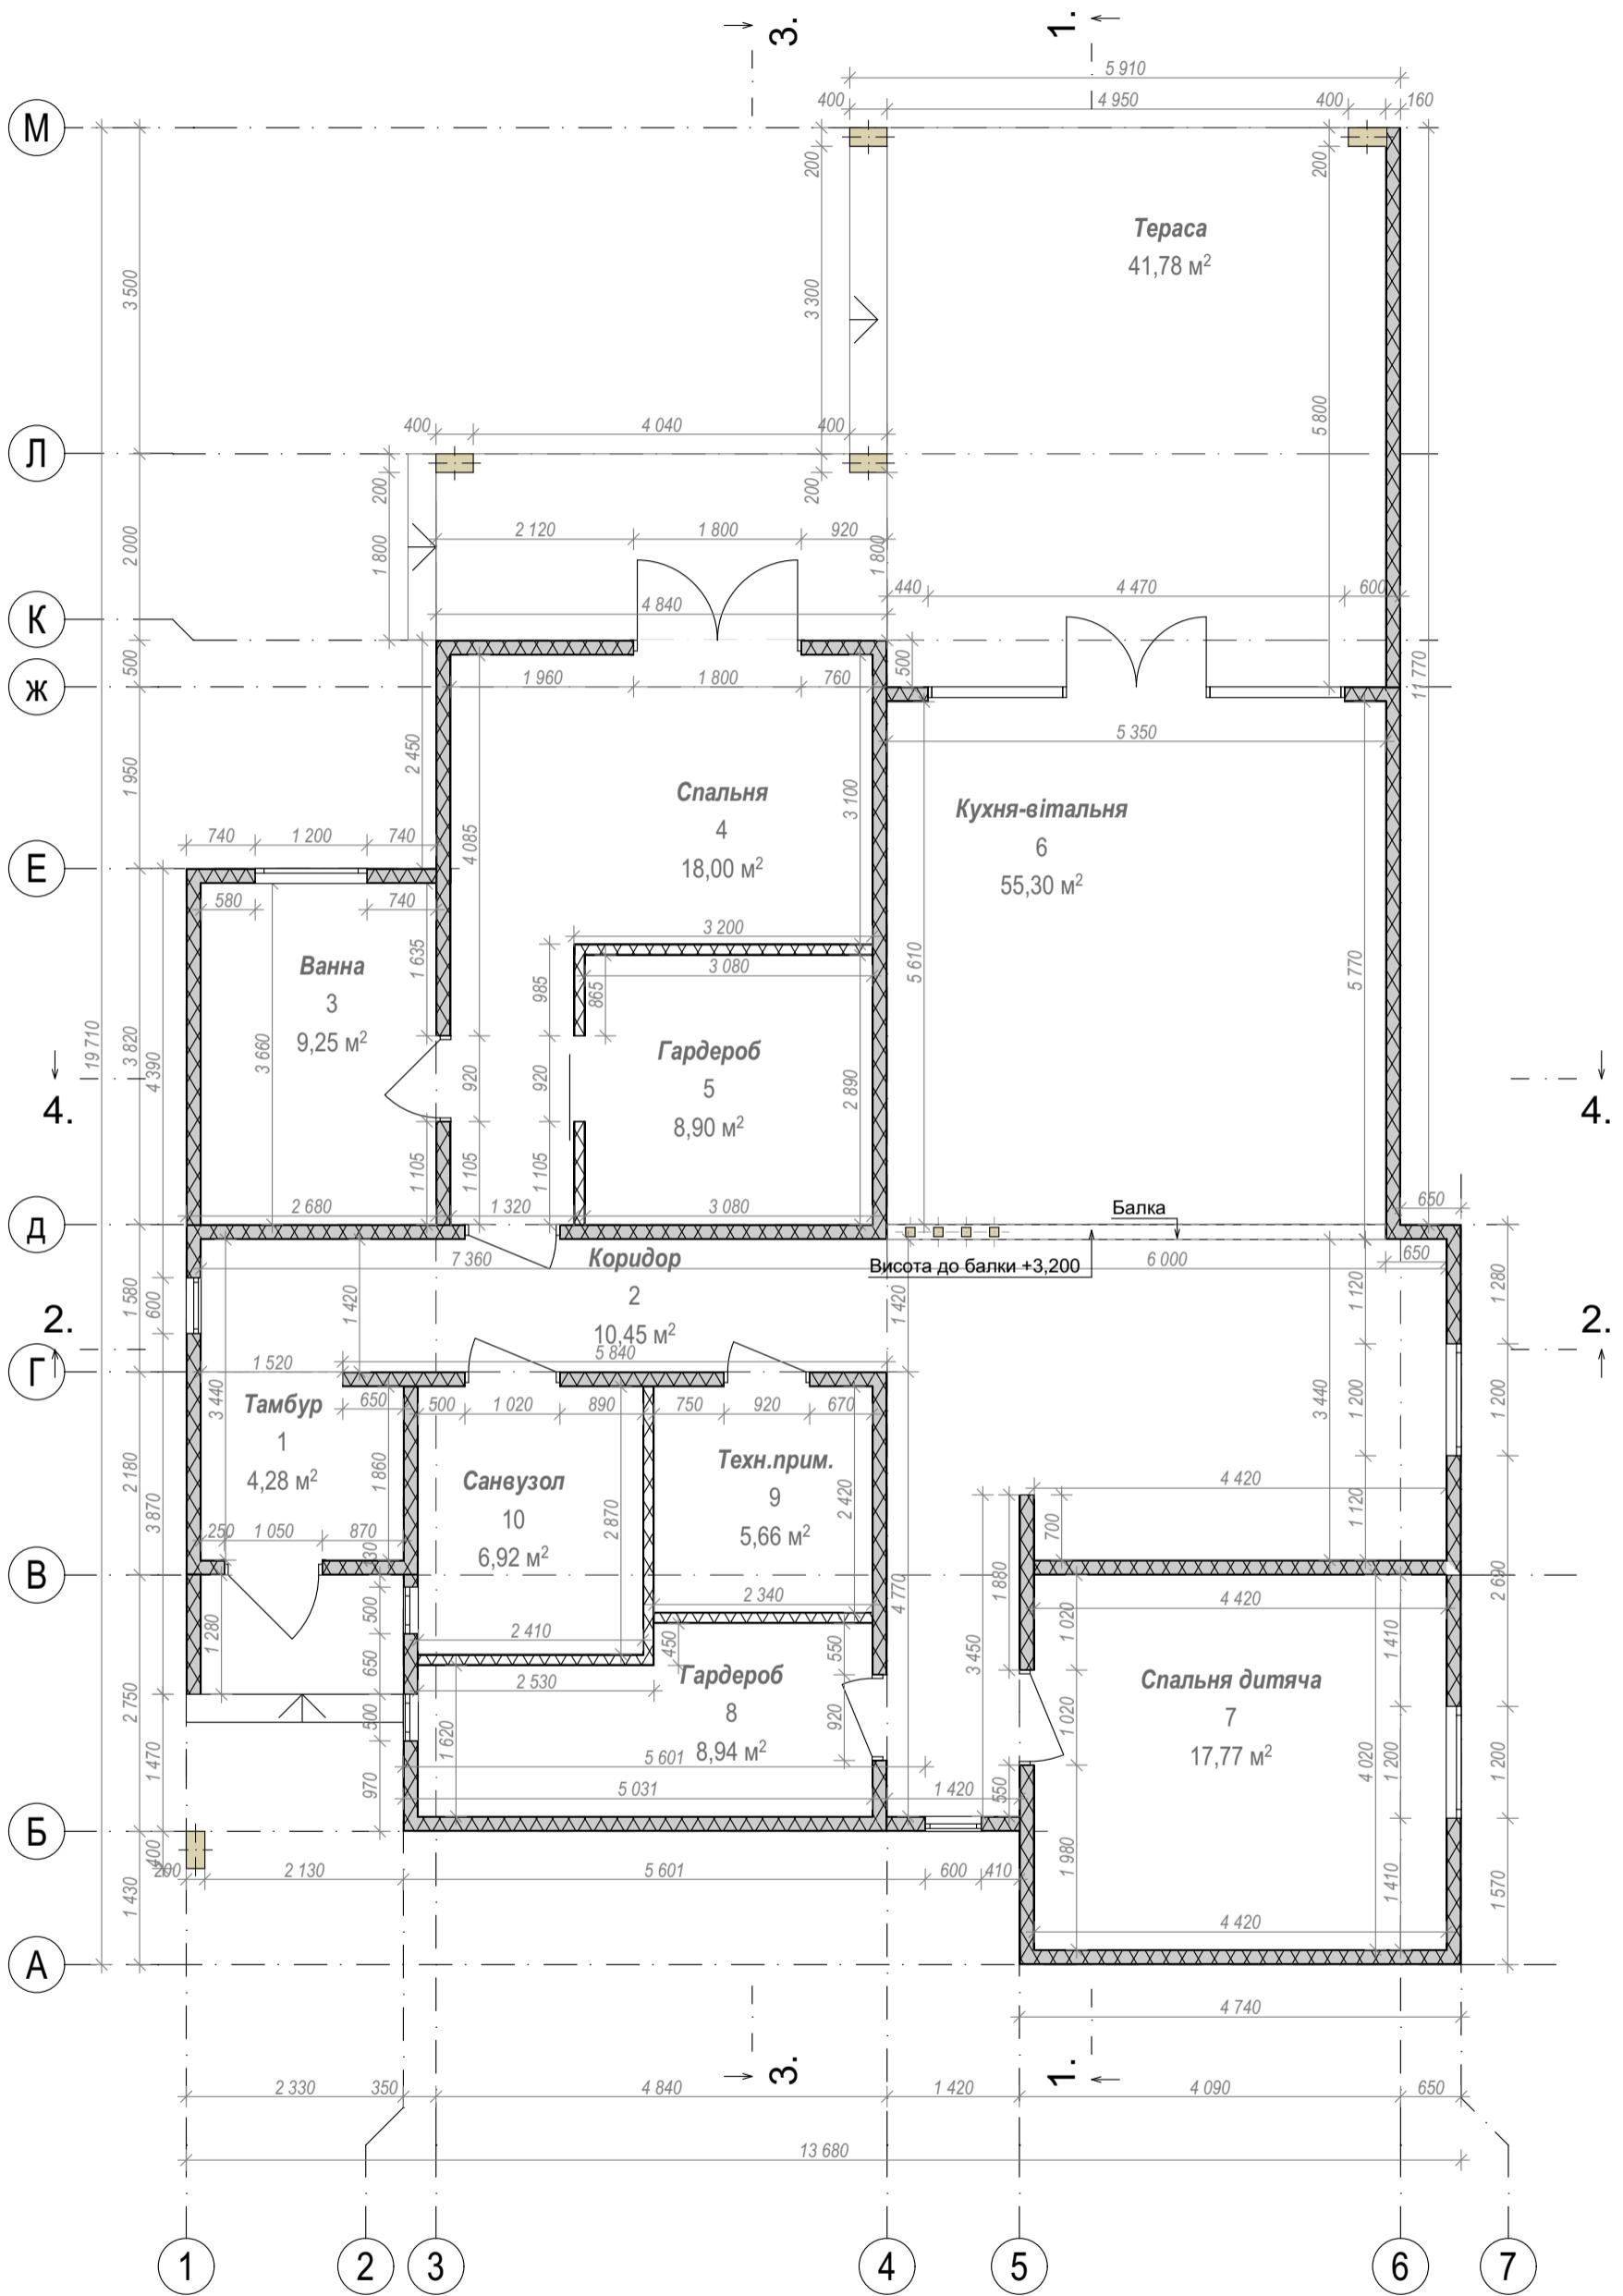

Змін.	Кіл.діл	Аркуш	№ Док.	Підпис
Виконав				
Перевірив				

Будівництво інвалідуального житлового будинку

Київська обл., Бучанський р-н,  
с. Віта Поштова

A modern, single-story house with a dark blue roof and light-colored walls, featuring large windows and doors, surrounded by landscaping.

План поверху на відмітці 0.000  
М1:75



**УКРСІПБУД**

М

Л

К

Е

Д

Г

В

Б

А

3.

1.

3.

4.

5.

1.

4.

2.

2.

1.


2.

3.

4.

6.

7.

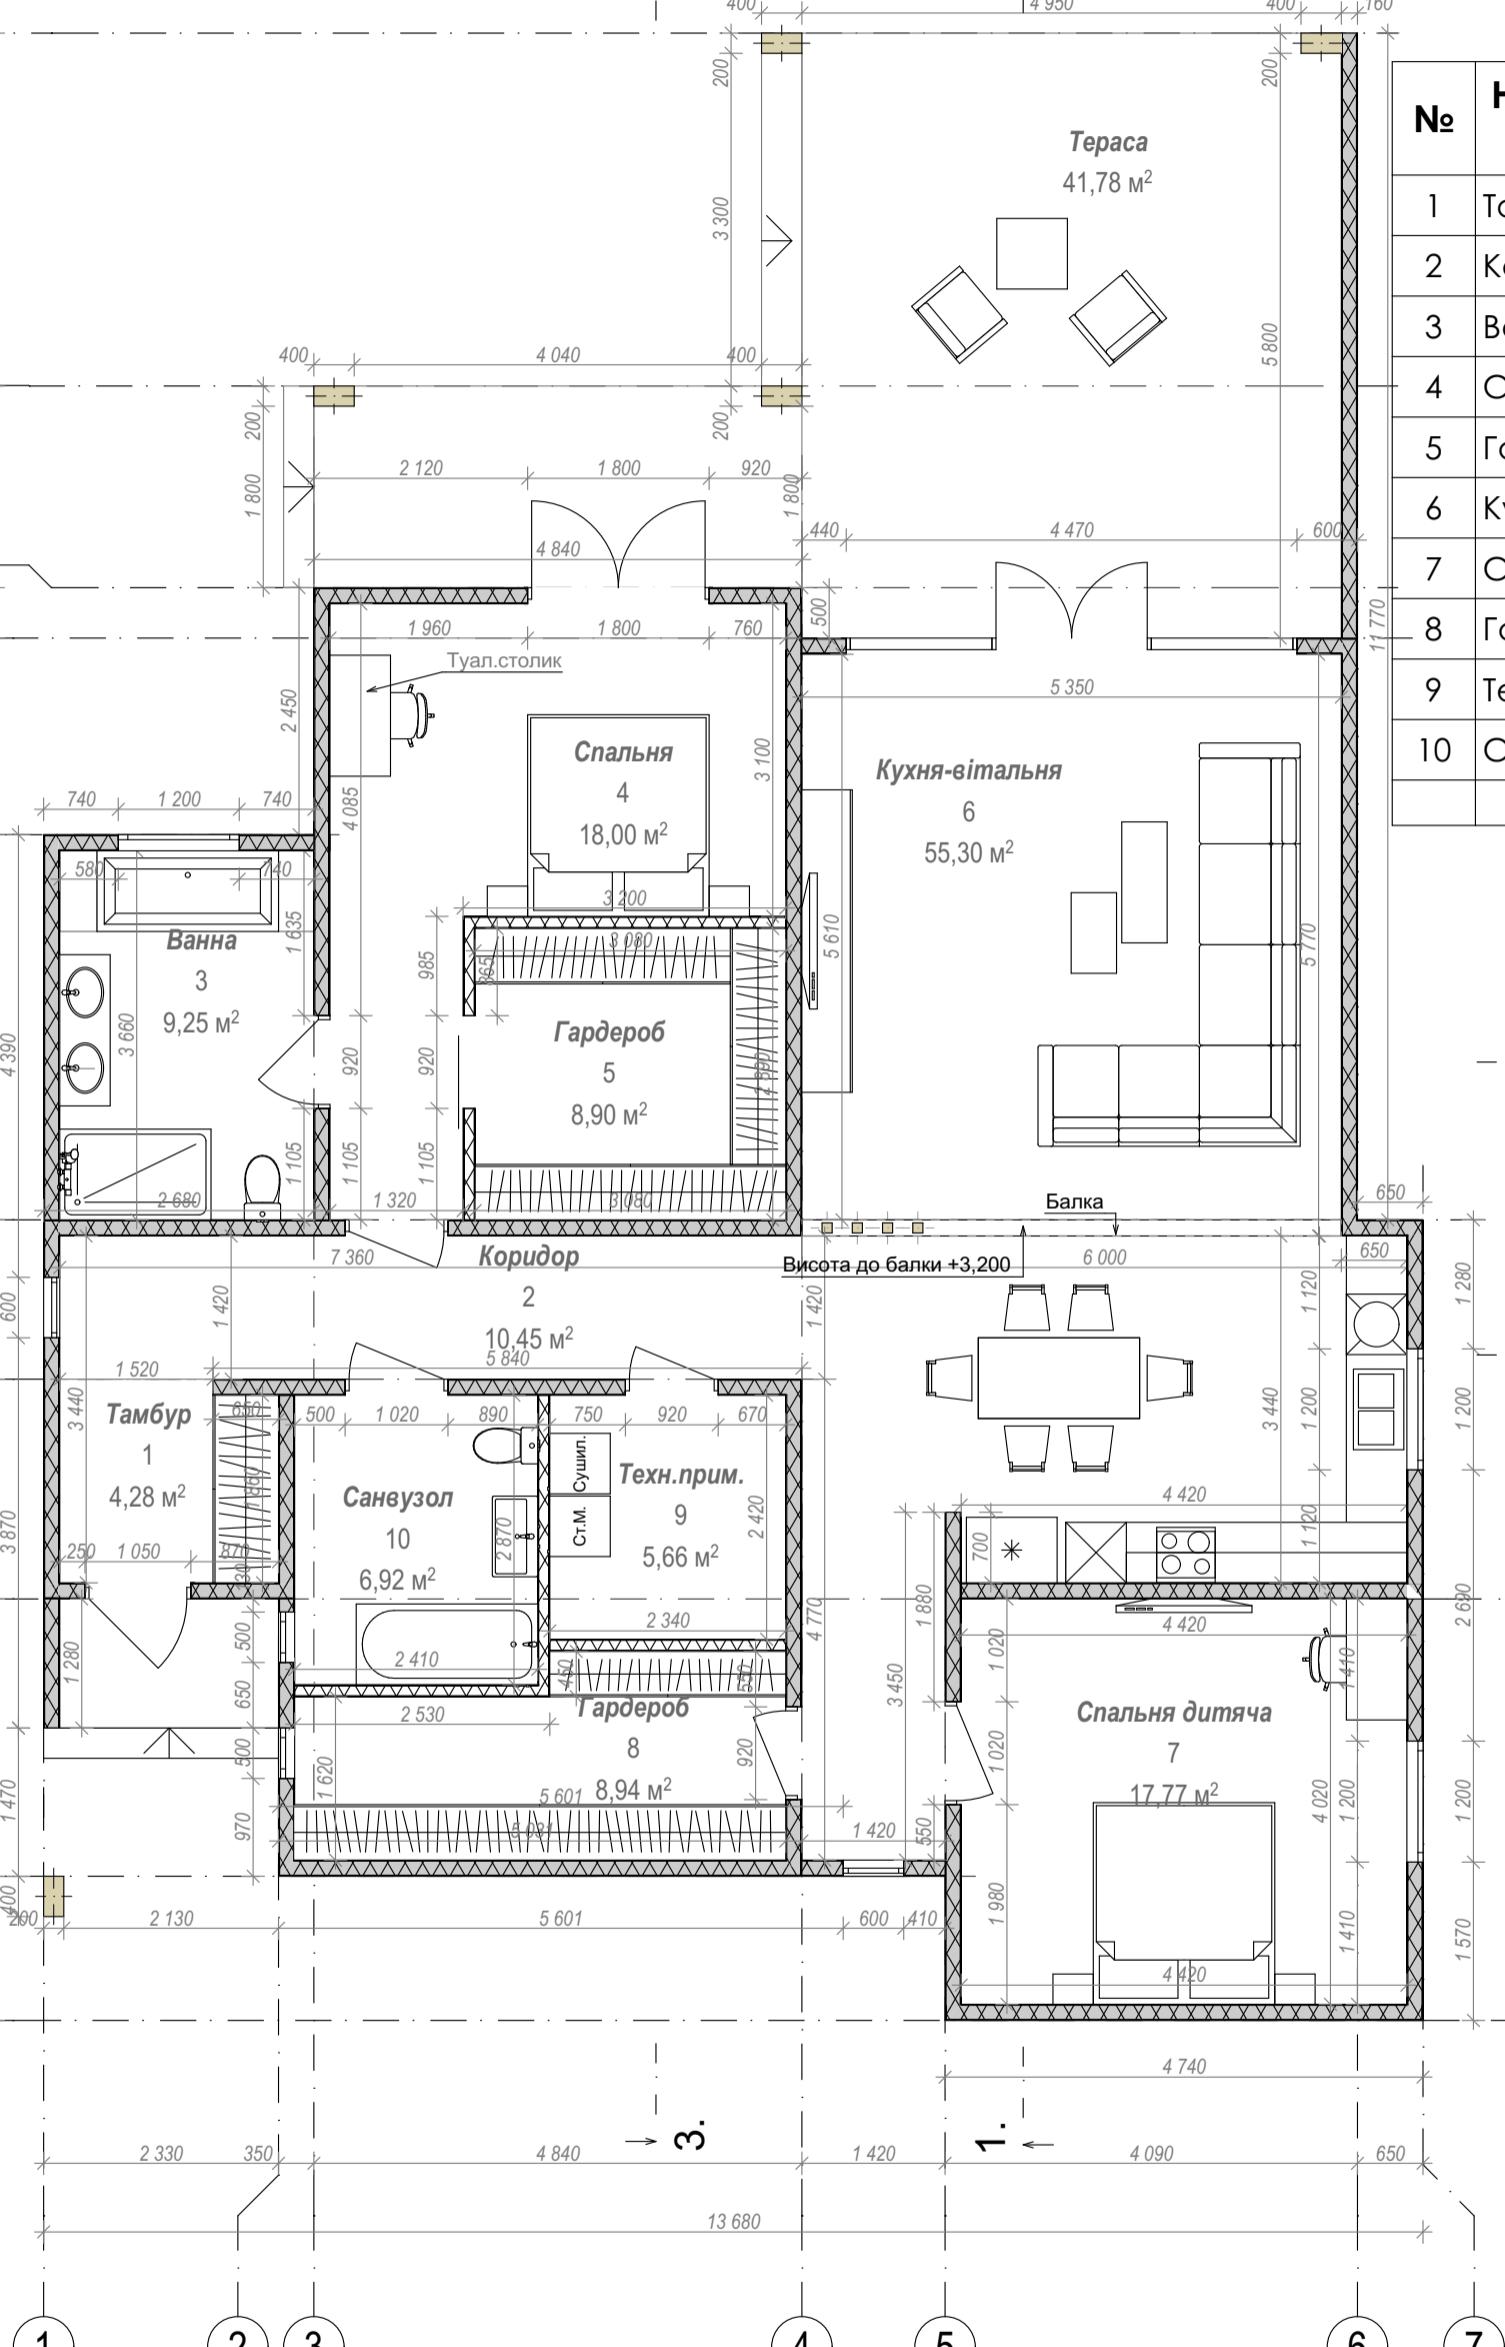

№	Найменування приміщення	Площа, м.кв.
1	Тамбур	4,28
2	Коридор	10,45
3	Ванна	9,25
4	Спальня	18,00
5	Гардероб	8,90
6	Кухня-вітальня	55,30
7	Спальня дитяча	17,77
8	Гардероб	8,94
9	Техн.прим.	5,66
10	Санвузол	6,92
		145,47 м <sup>2</sup>

Будівництво індивідуального житлового будинку				
Змін.	Кіл.діл.	Аркуш	№ Док.	Підпис
Виконав				
Перевірив				
План розташування меблів та сантехніки				
Київська обл., Бучанський р-н, с. Віта Поштова				Стадія Аркуш Аркушів ЕП 6

М

Л

К

Ж

Е

4.

Д

2.

Г

В

Б

А

1

2

3

4

5

6

7

Тераса  
41,78 м<sup>2</sup>

Спальня  
4  
18,00 м<sup>2</sup>  
Кухня-вітальня  
6  
55,30 м<sup>2</sup>

+3,200  
Гардероб  
5  
8,90 м<sup>2</sup>

+3,200  
Ванна  
3  
9,25 м<sup>2</sup>

ДО-03

ДО-02

ДО-04

ДО-05

ДО-06

Балка

Висота до балки +3,200

ДО-01

ДО-02

ДО-23

ДО-24

ДО-25

ДО-26

ДО-27

ДО-28

ДО-29

ДО-30

ДО-31

ДО-32

ДО-33

ДО-34

ДО-35

ДО-36

ДО-37

ДО-38

ДО-39

ДО-40

ДО-41

ДО-42

ДО-43

ДО-44

ДО-45

ДО-46

ДО-47

ДО-48

ДО-49

ДО-50

ДО-51

ДО-52

ДО-53

ДО-54

ДО-55

ДО-56

ДО-57

ДО-58

ДО-59

ДО-60

ДО-61

ДО-62

ДО-63

ДО-64

ДО-65

ДО-66

ДО-67

ДО-68

ДО-69

ДО-70

ДО-71

ДО-72

ДО-73

ДО-74

ДО-75

ДО-76

ДО-77

ДО-78

ДО-79

ДО-80

ДО-81

ДО-82

ДО-83

ДО-84

ДО-85

ДО-86

ДО-87

ДО-88

ДО-89

ДО-90

ДО-91

ДО-92

ДО-93

ДО-94

ДО-95

ДО-96

ДО-97

ДО-98

ДО-99

ДО-100

ДО-101

ДО-102

ДО-103

ДО-104

ДО-105

ДО-106

ДО-107

ДО-108

ДО-109

ДО-110

ДО-111

ДО-112

ДО-113

ДО-114

ДО-115

ДО-116

ДО-117

ДО-118

ДО-119

ДО-120

ДО-121

ДО-122

ДО-123

ДО-124

ДО-125

ДО-126

ДО-127

ДО-128

ДО-129

ДО-130

ДО-131

ДО-132

ДО-133

ДО-134

ДО-135

ДО-136

ДО-137

ДО-138

ДО-139

ДО-140

ДО-141

ДО-142

ДО-143

ДО-144

ДО-145

ДО-146

ДО-147

ДО-148

ДО-149

ДО-150

ДО-151

ДО-152

ДО-153

ДО-154

ДО-155

ДО-156

ДО-157

ДО-158

ДО-159

ДО-160

ДО-161

ДО-162

ДО-163

ДО-164

ДО-165

ДО-166

ДО-167

ДО-168

ДО-169

ДО-170

ДО-171

ДО-172

ДО-173

ДО-174

ДО-175

ДО-176

ДО-177

ДО-178

ДО-179

ДО-180

ДО-181

ДО-182

ДО-183

ДО-184

ДО-185


ДО-186

ДО-187

ДО-188&lt;/div

Умовні позначення:


контур будівлі  
 контур парапету на відмітці +3,900

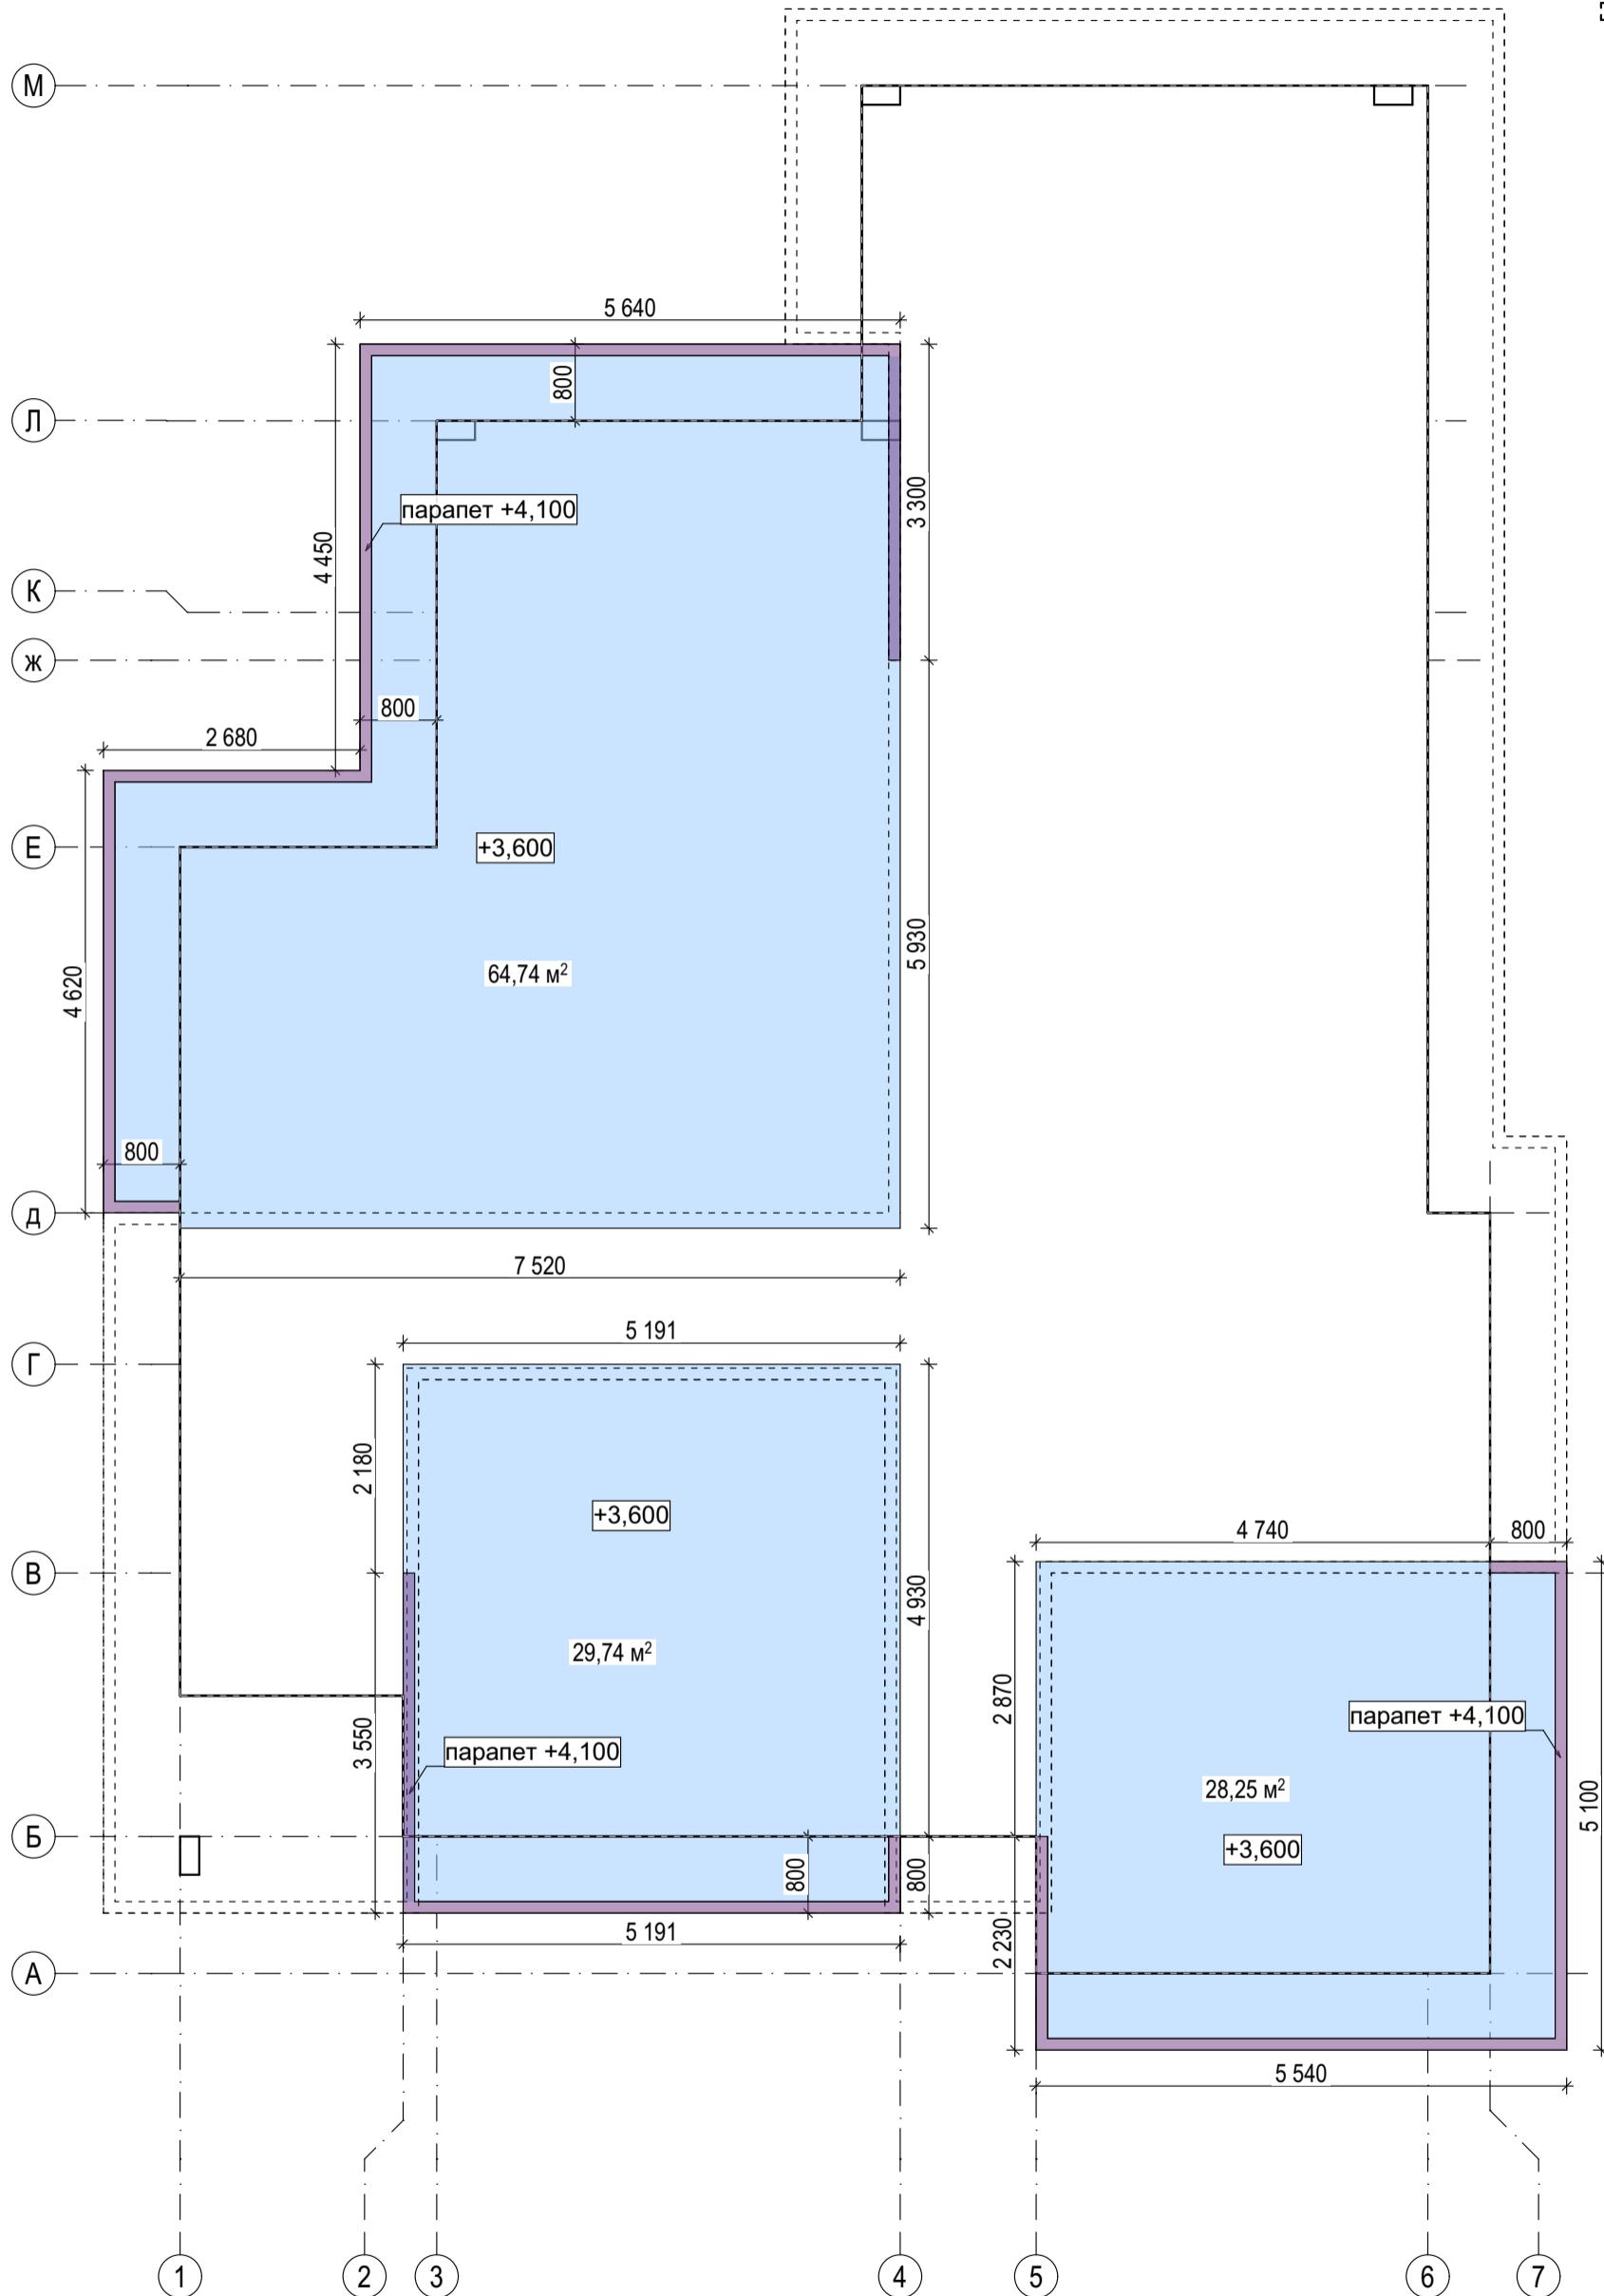

Будівництво індивідуального житлового будинку				
Змін.	Кіл.діл.	Аркуш	№ Док.	Підпис
				Київська обл., Бучанський р-н, с. Віта Поштова
				Стадія Аркуш Аркушів ЕП 8
Виконав				
Перевірив				
План даху на відмітці +3,600				
<b>УКРСІПБУД</b>				

Умовні позначення:


контур будівлі  
контур парапету на відмітці +3,600

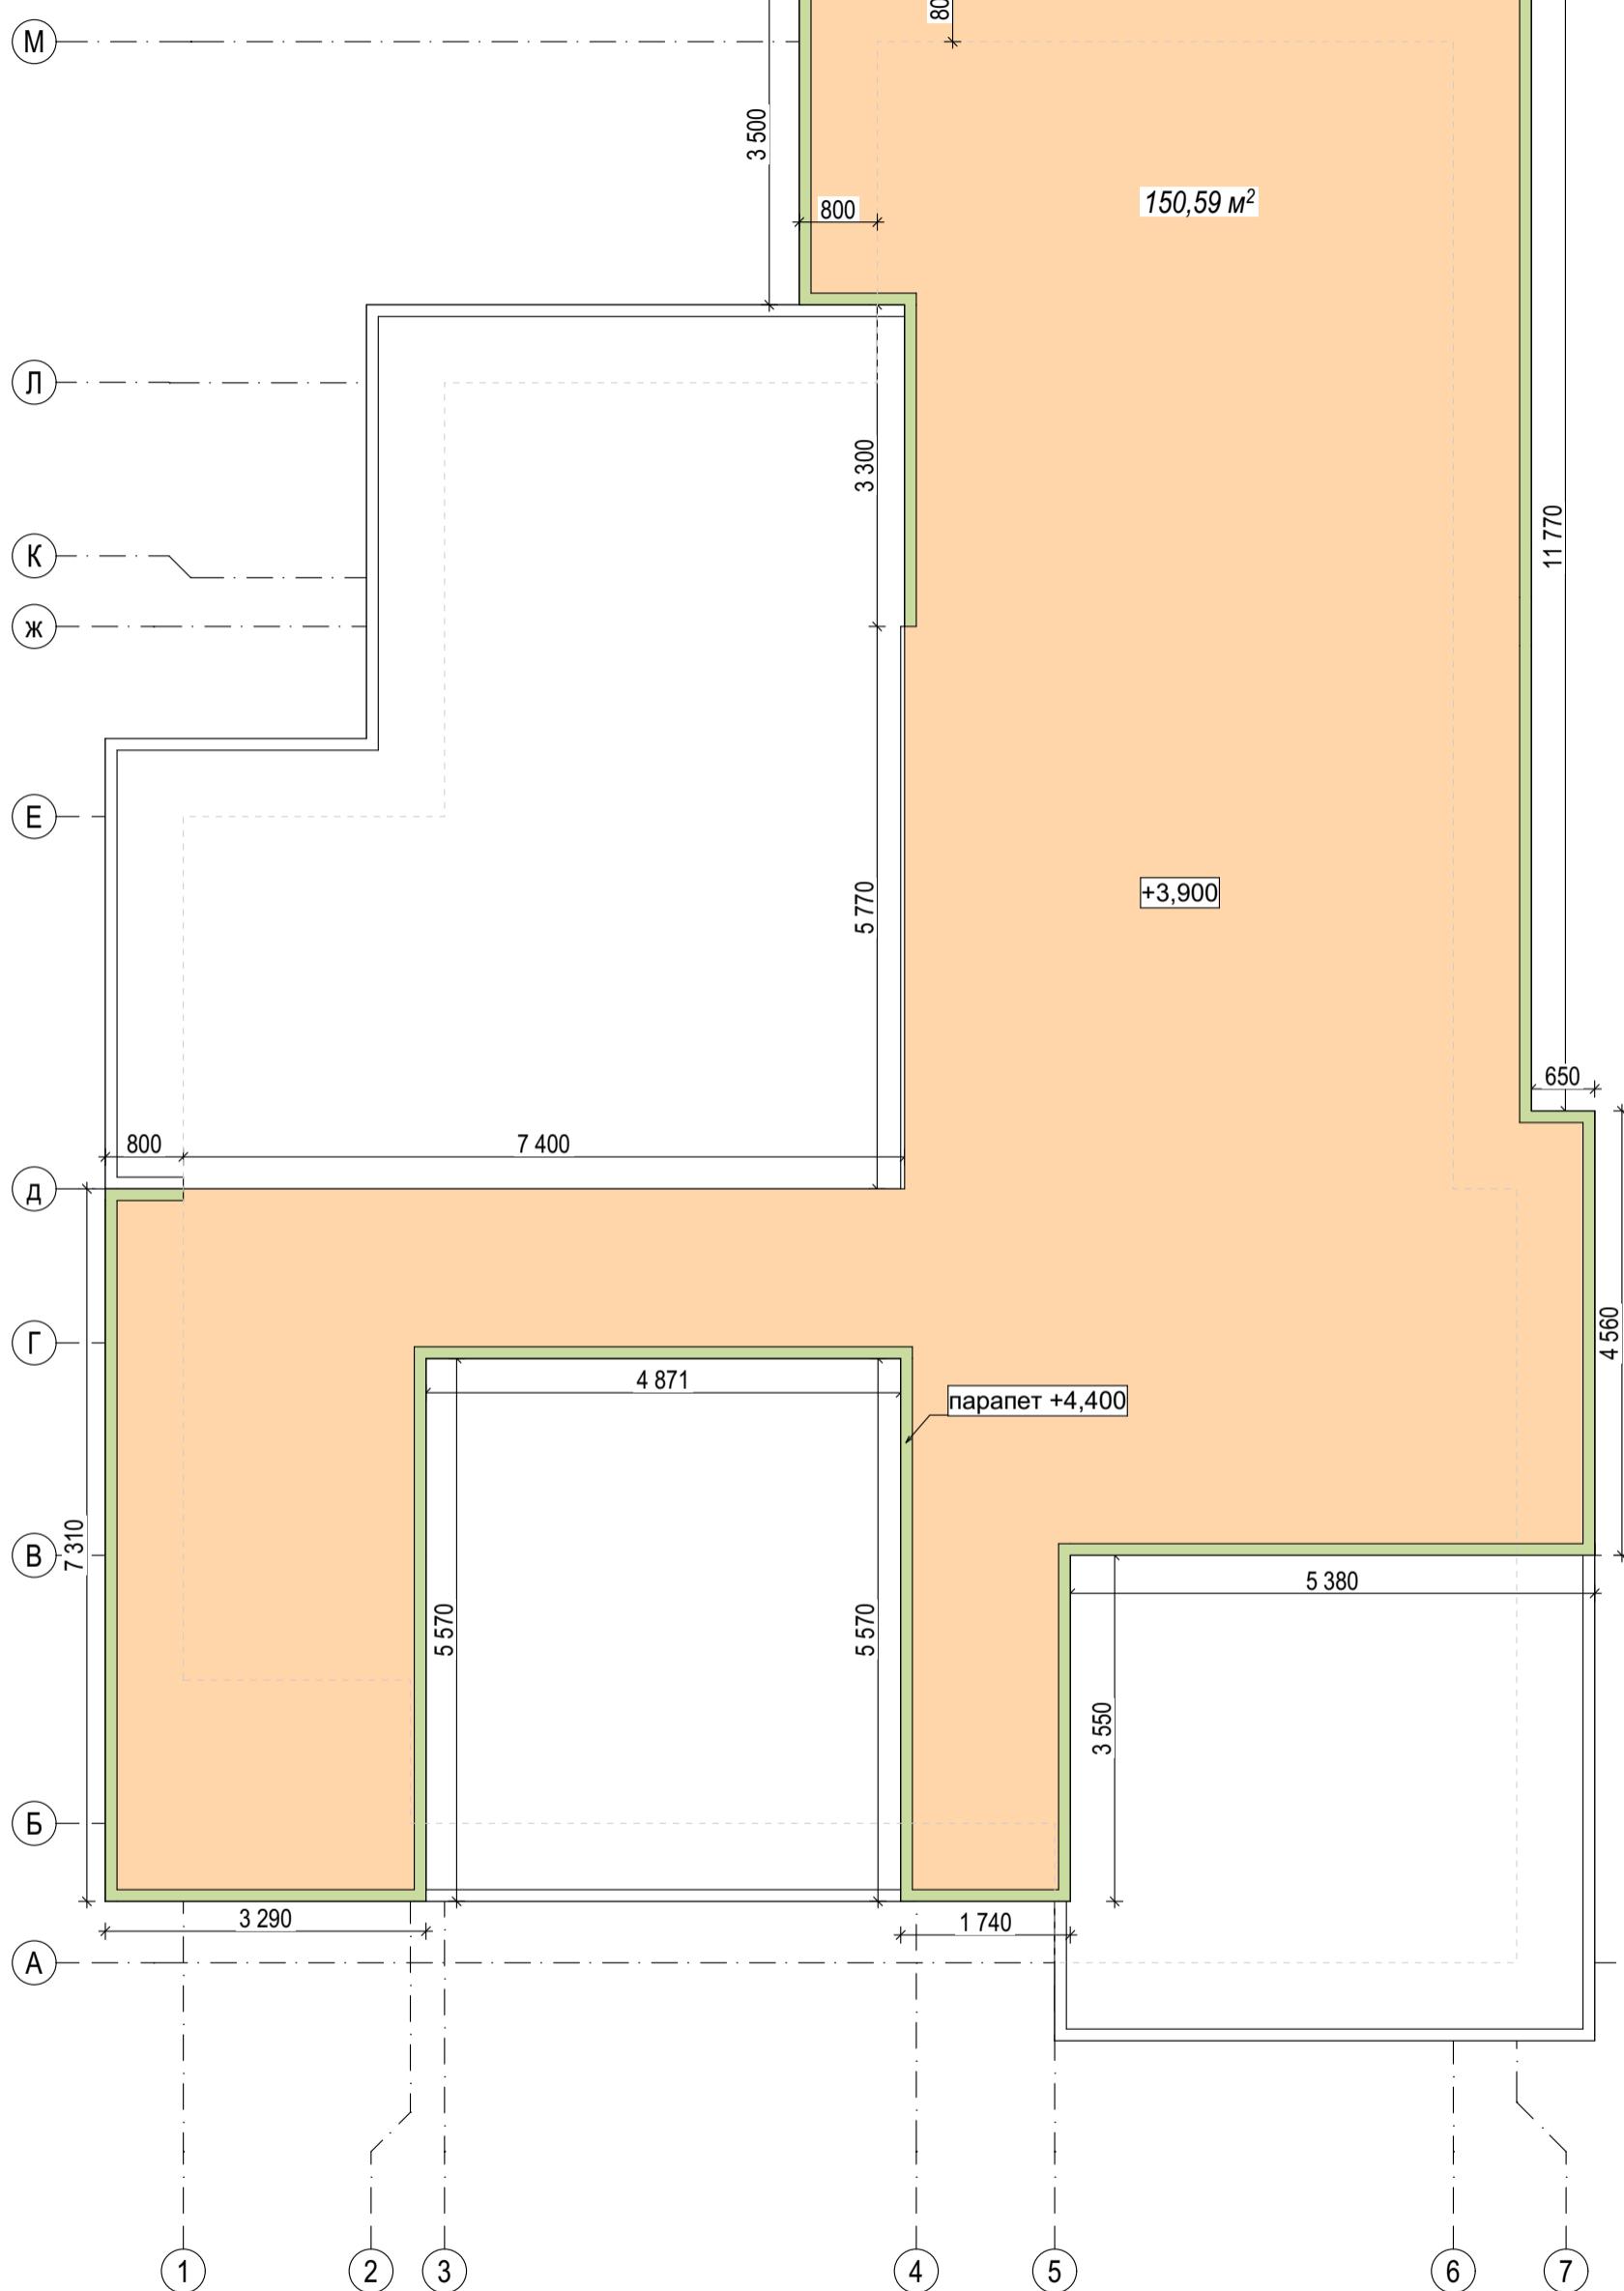

					Будівництво індивідуального житлового будинку		
Змін.	Кіл.діл	Аркуш	№ Док.	Підпис	Київська обл., Бучанський р-н, с. Віта Поштова		
Виконав					Стадія		
Перевірив					Аркуш		
					Аркушів		
					ЕП		
План даху на відмітці +3,900							
					<b>УКРСІПБУД</b>		

Умовні позначення:

контур парапету

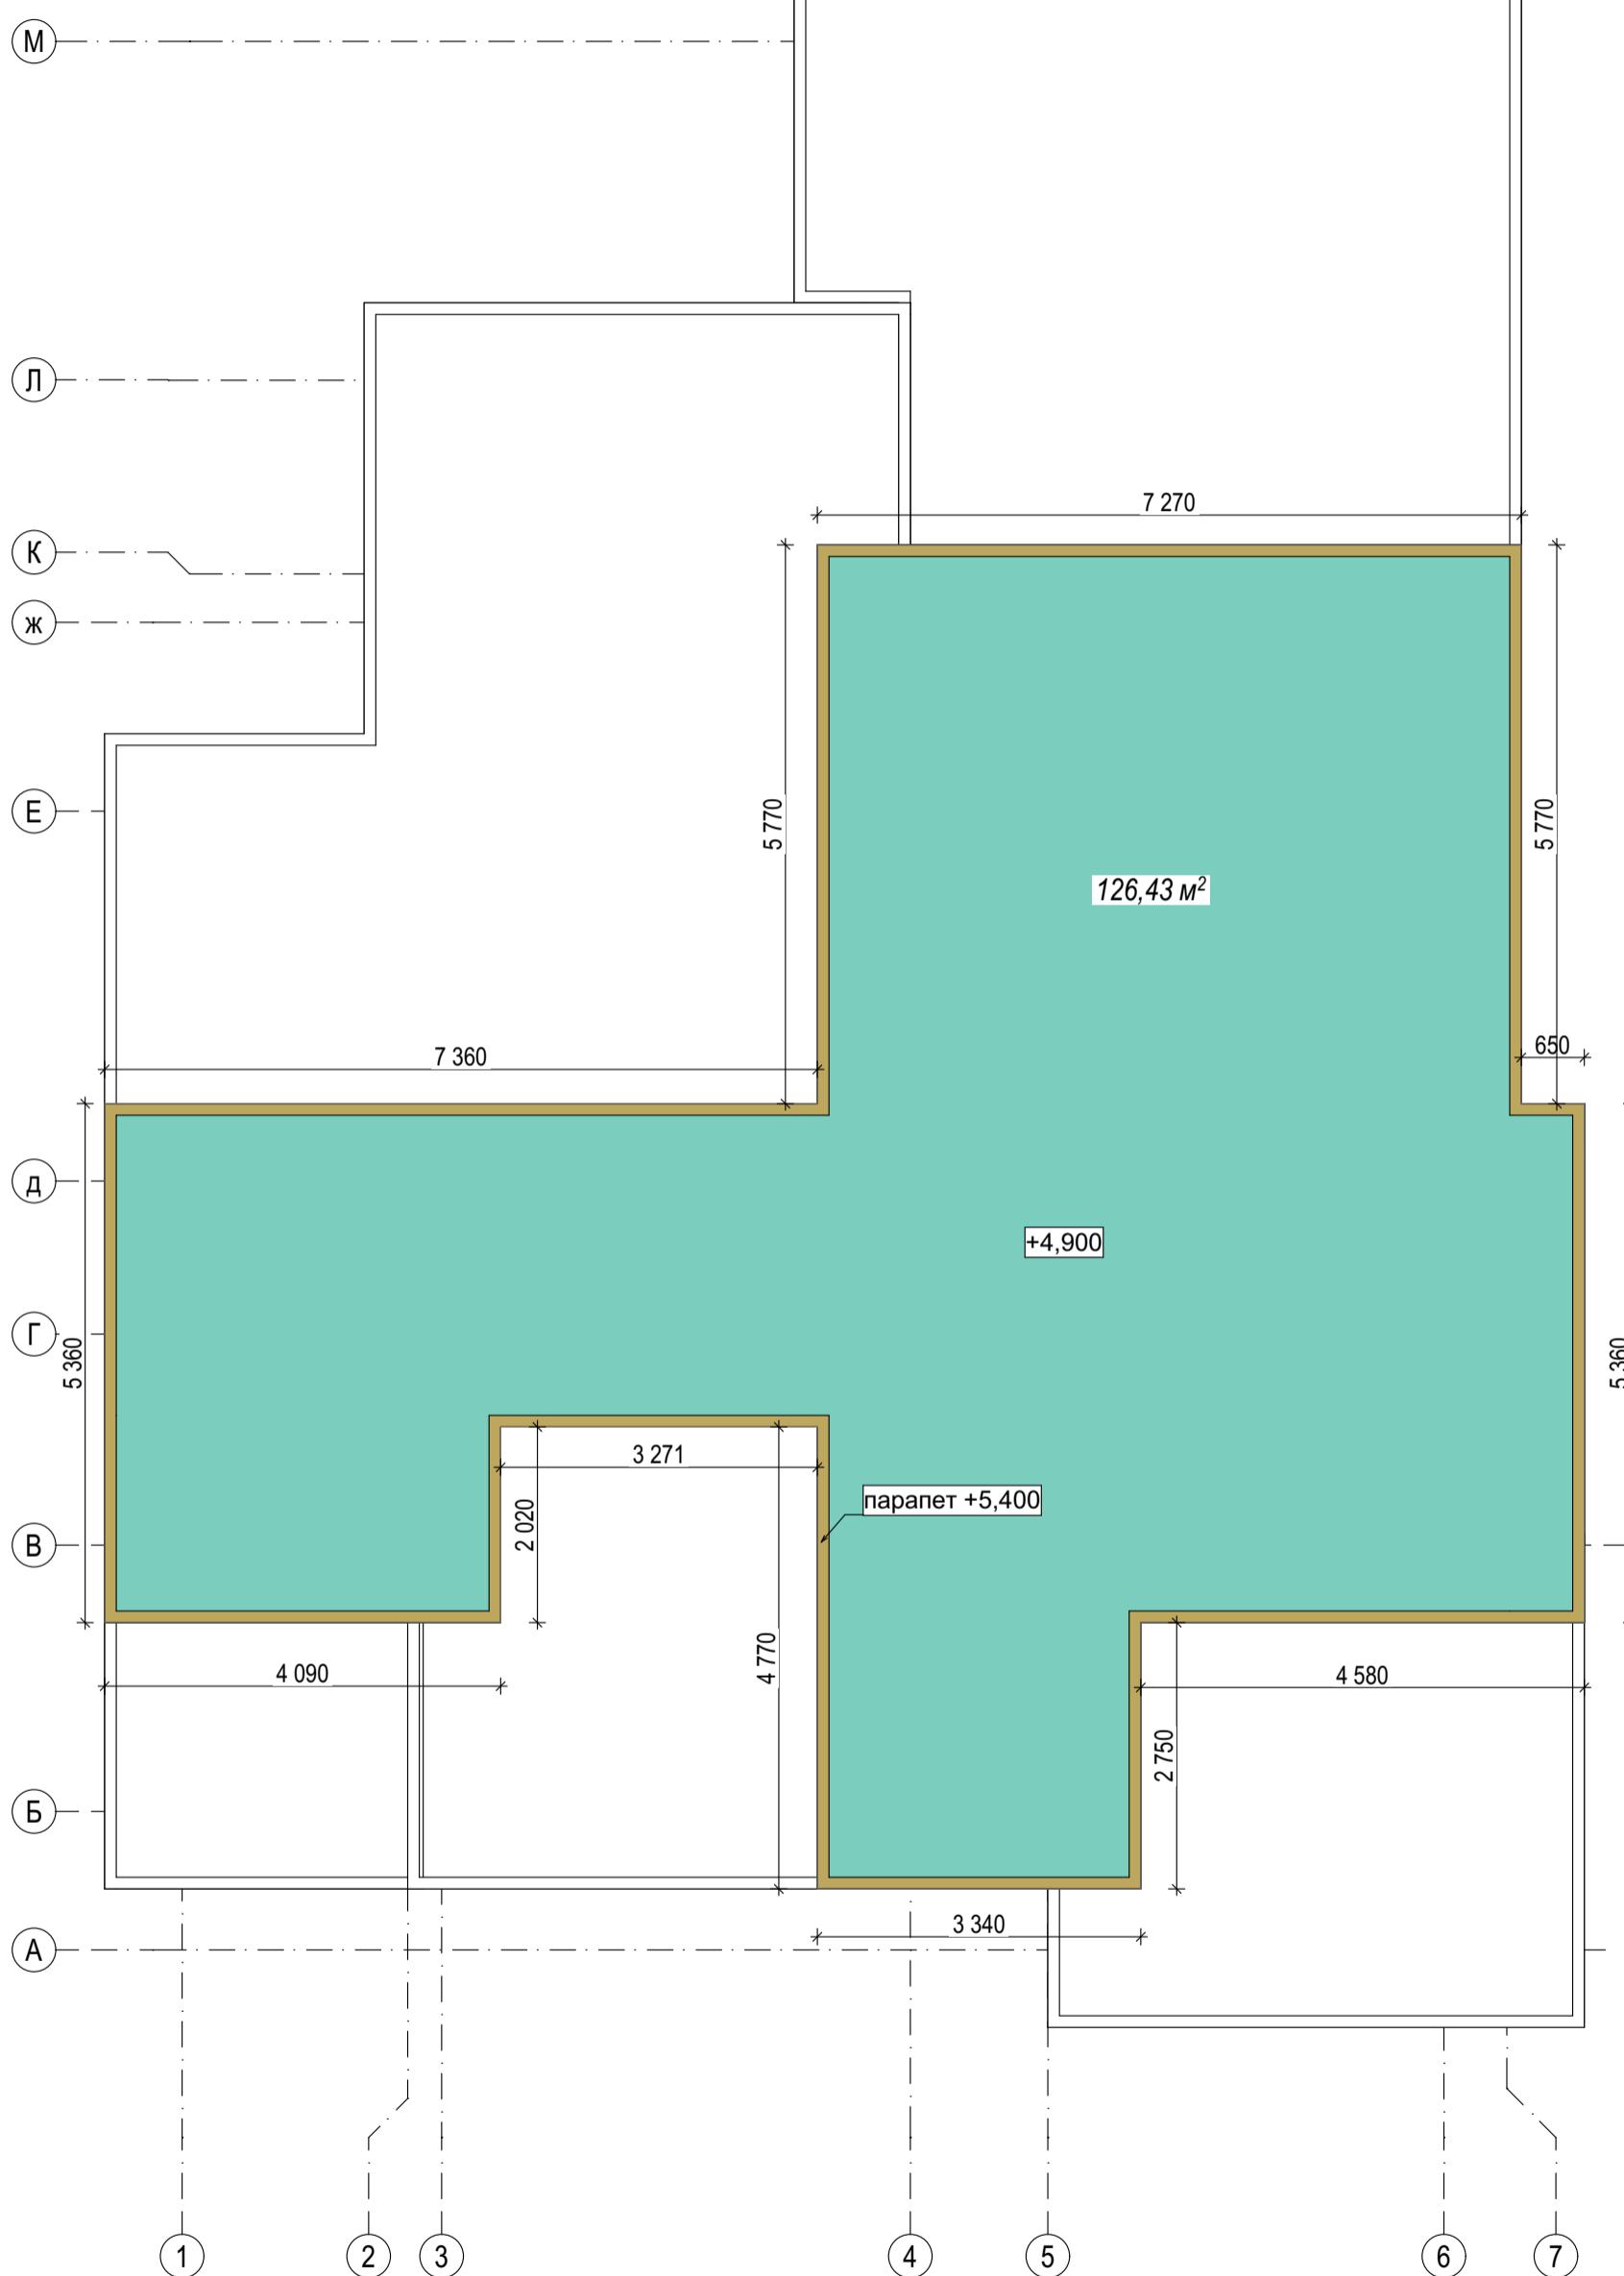

Змін.	Кіл.діл.	Аркуш	№ Док.	Підпис
Виконав				
Перевірив				

Будівництво індивідуального житлового будинку

Київська обл., Бучанський р-н,  
с. Віта Поштова


Стадія Аркуш Аркушів  
ЕП 10

План даху на відмітці +5,400





УкрСіпБуд

Розріз 1-1

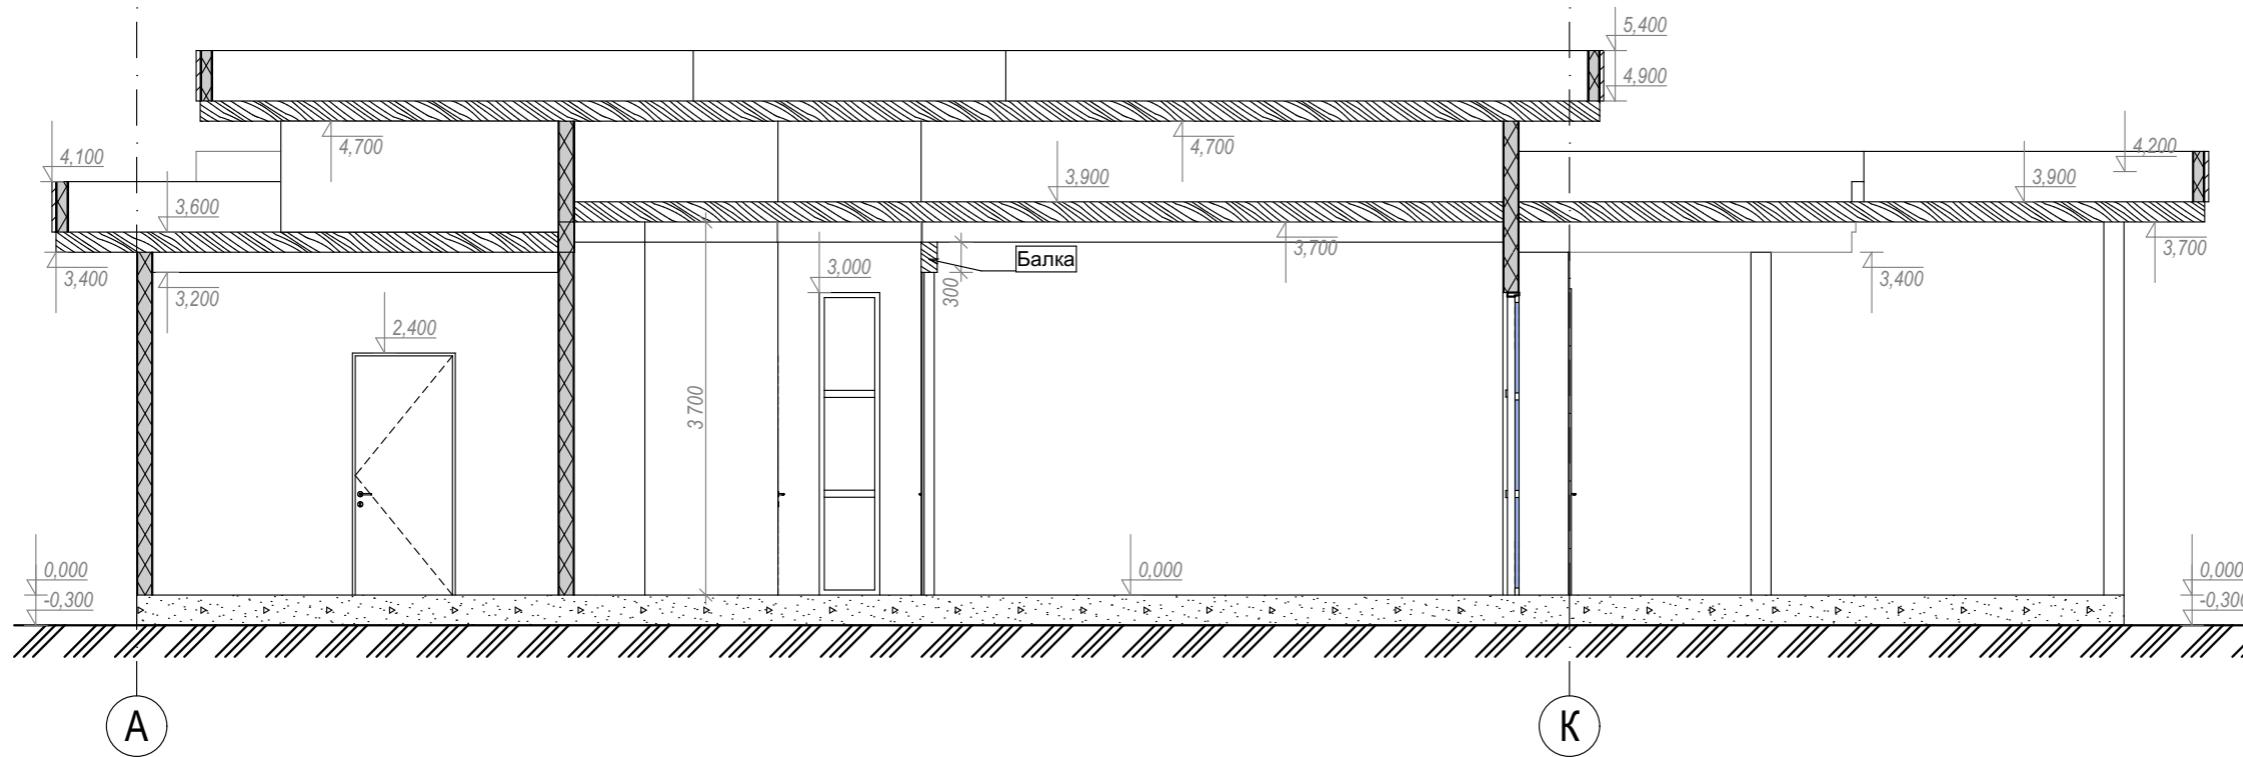


Розріз 2-2

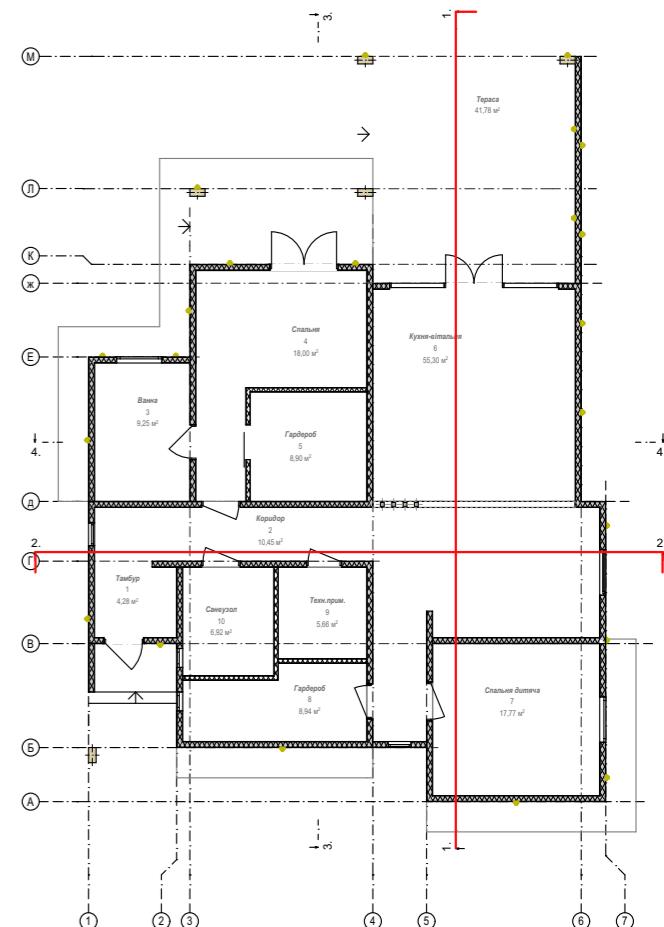
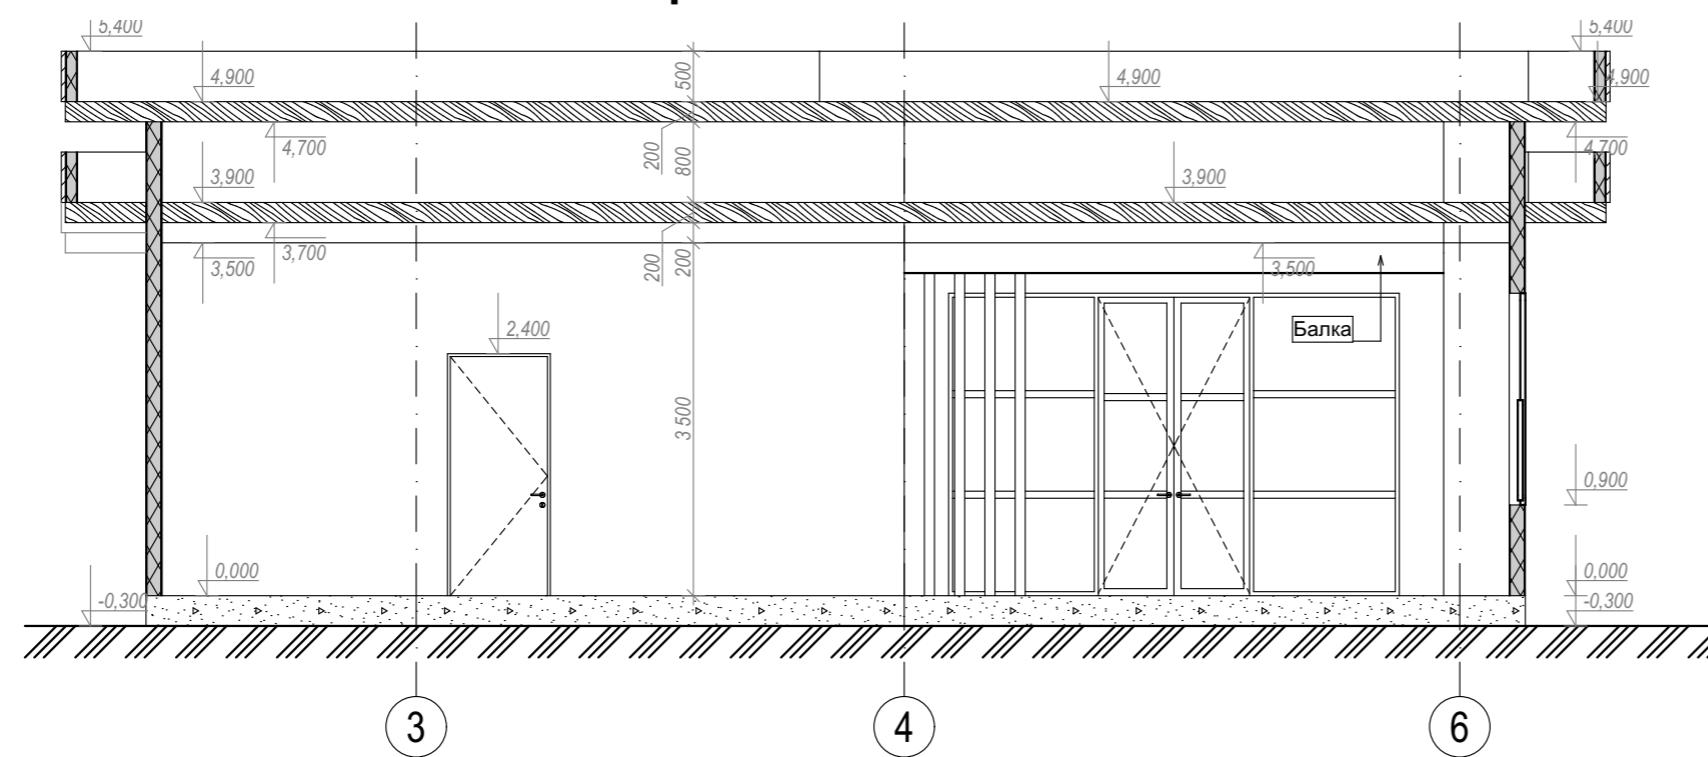



					Будівництво індивідуального житлового будинку		
Змін.	Кіл.діл	Аркуш	№ Док.	Pідпис	Kиївська обл., Бучанський р-н, с. Віта Поштова	Стадія	Аркуш
Виконав			Розріз 1-1, Розріз 2-2			EП	11
Перевірив						УКРСІПБУД	

Розріз 3-3

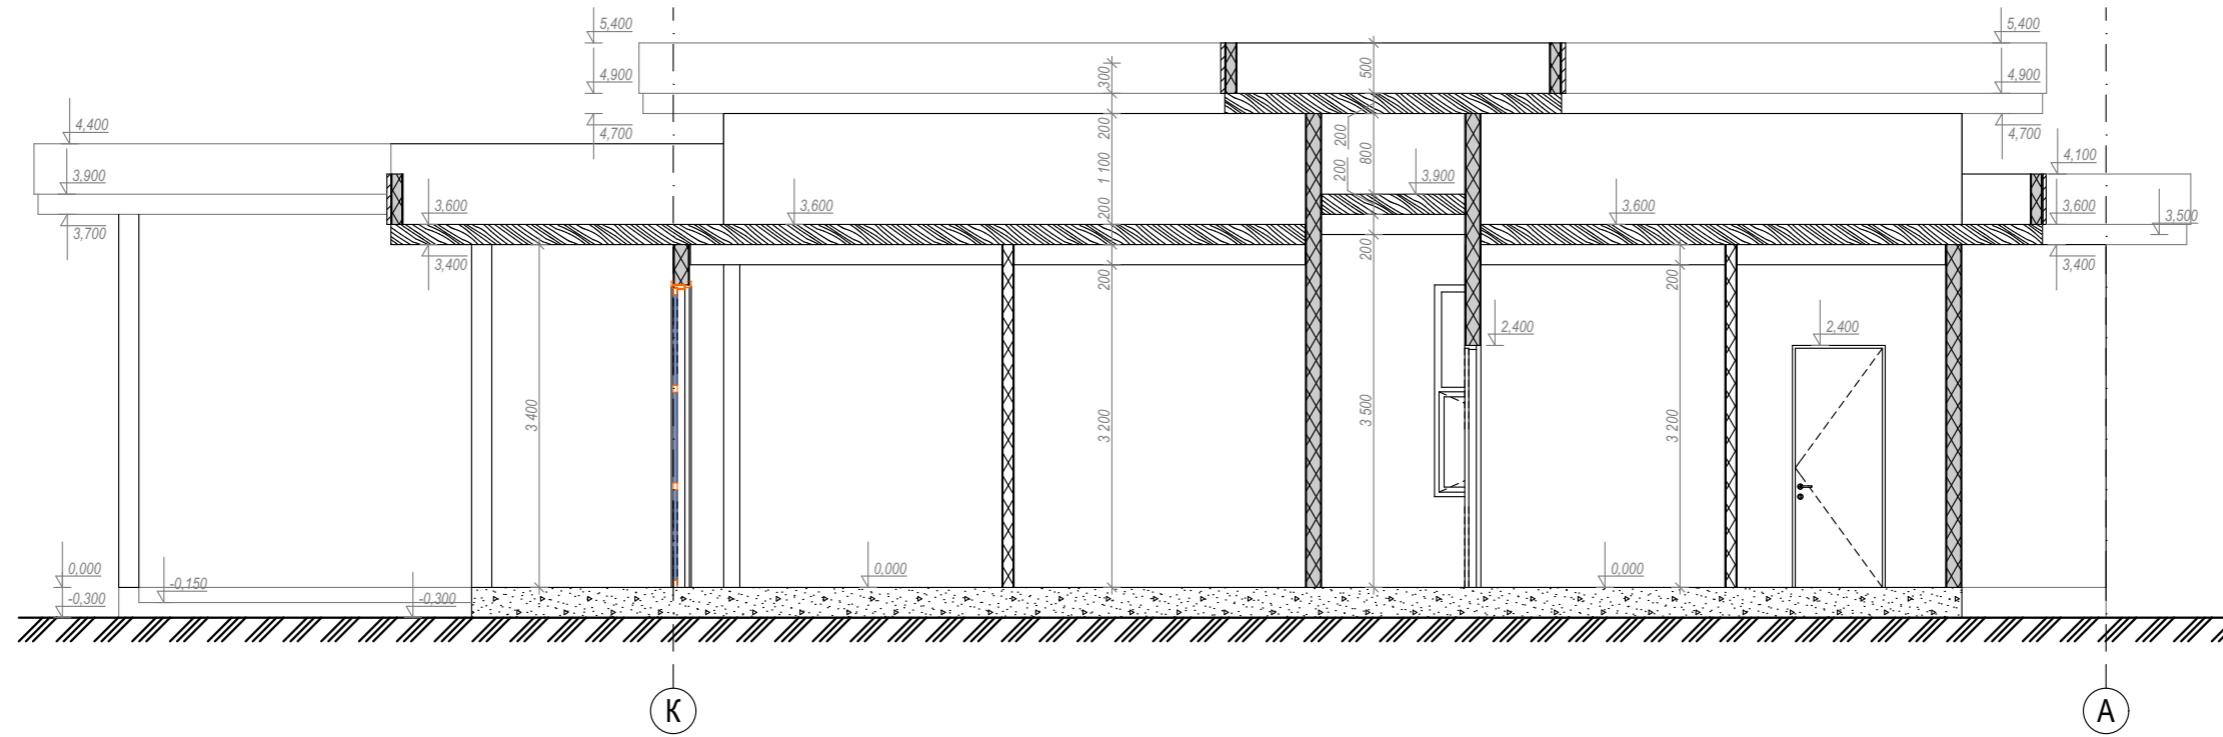


Розріз 4-4

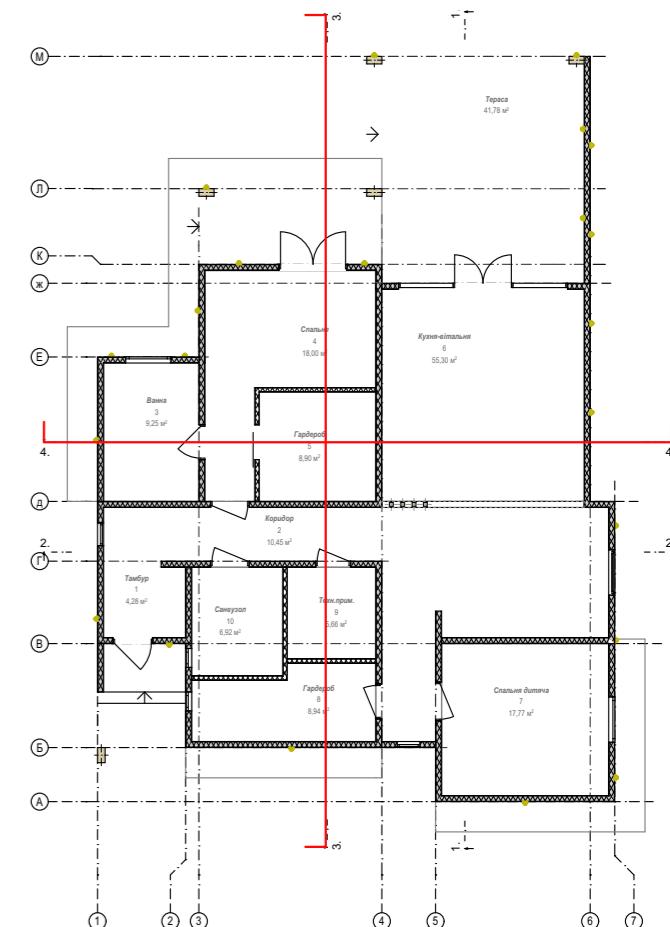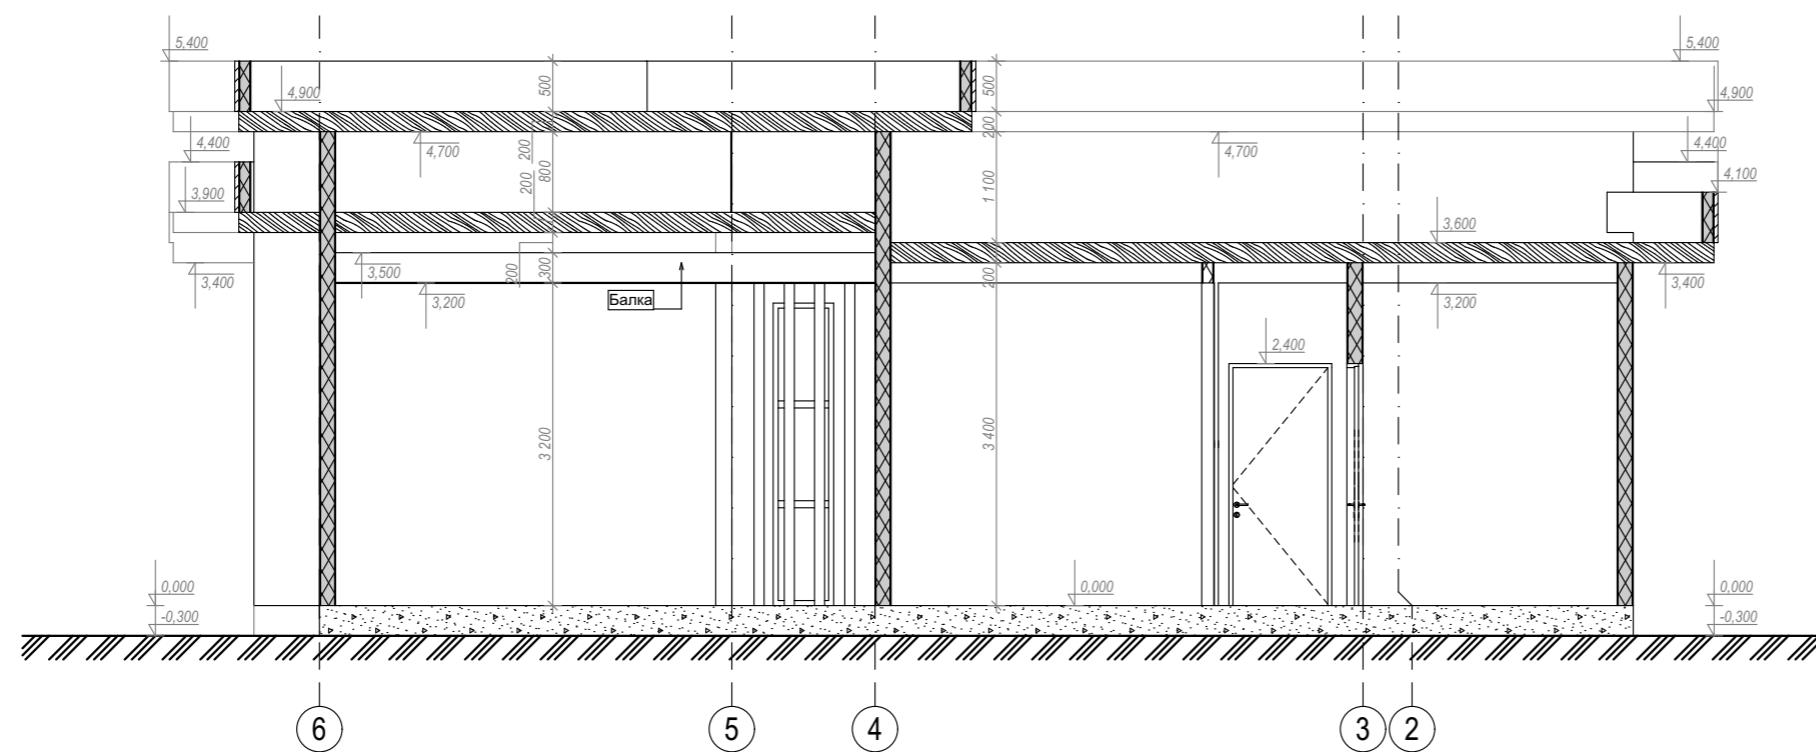


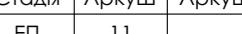
					Будівництво індивідуального житлового будинку		
					Kиївська обл., Бучанський р-н, с. Віта Поштова	Стадія	Аркуш
Змін.	Кіл.діл	Аркуш	№ Док.	Підпис		ЕП	11
Виконав					Розріз 3-3. Розріз 4-4		
Перевірив					 <b>УКРСІПБУД</b>		

Фасад 1-7

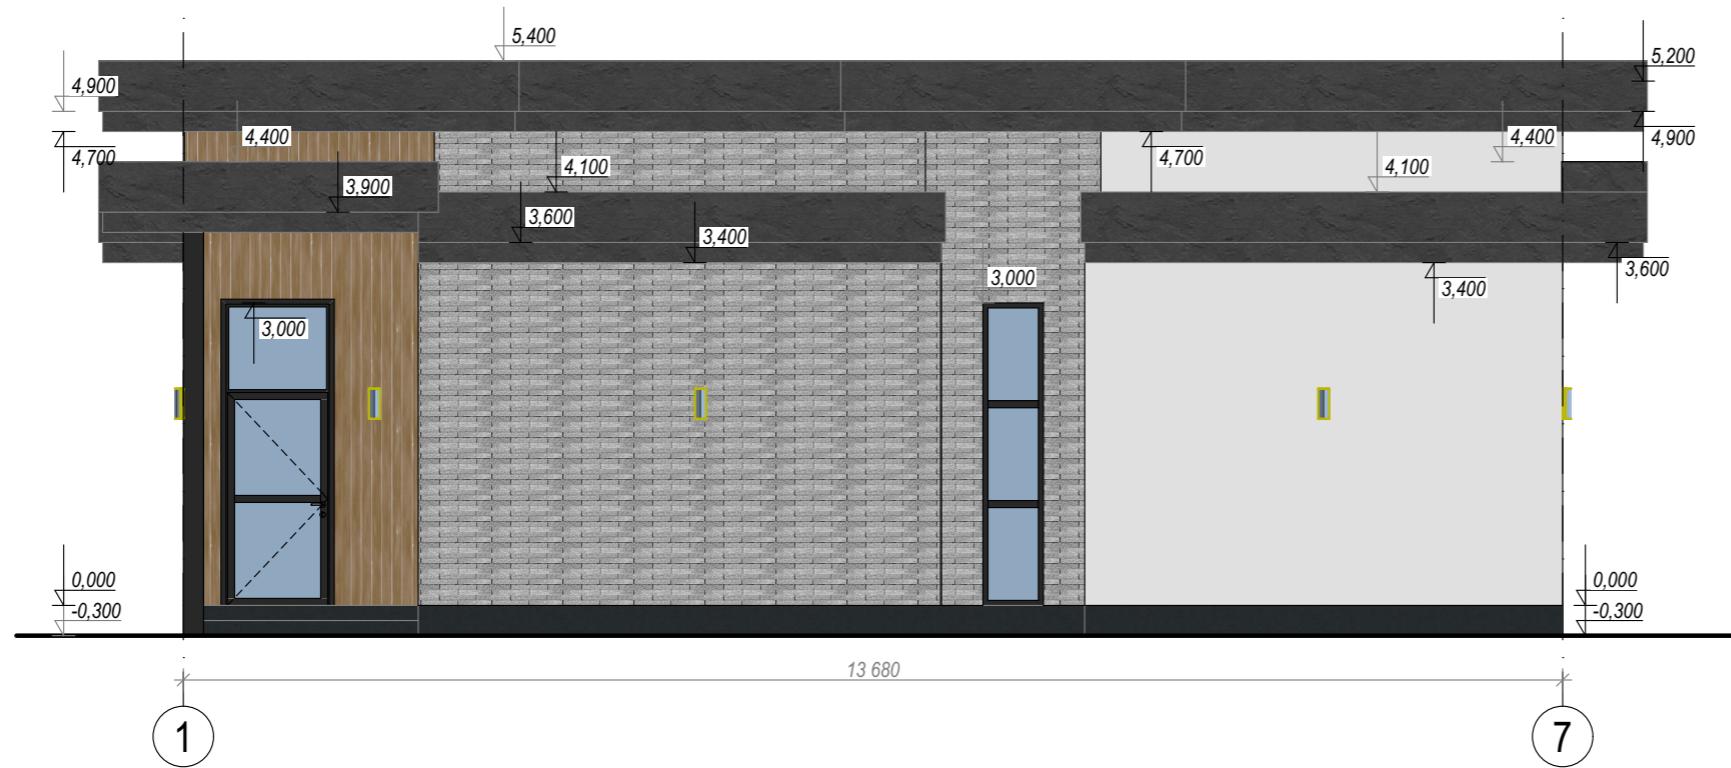

Фасад 7-1


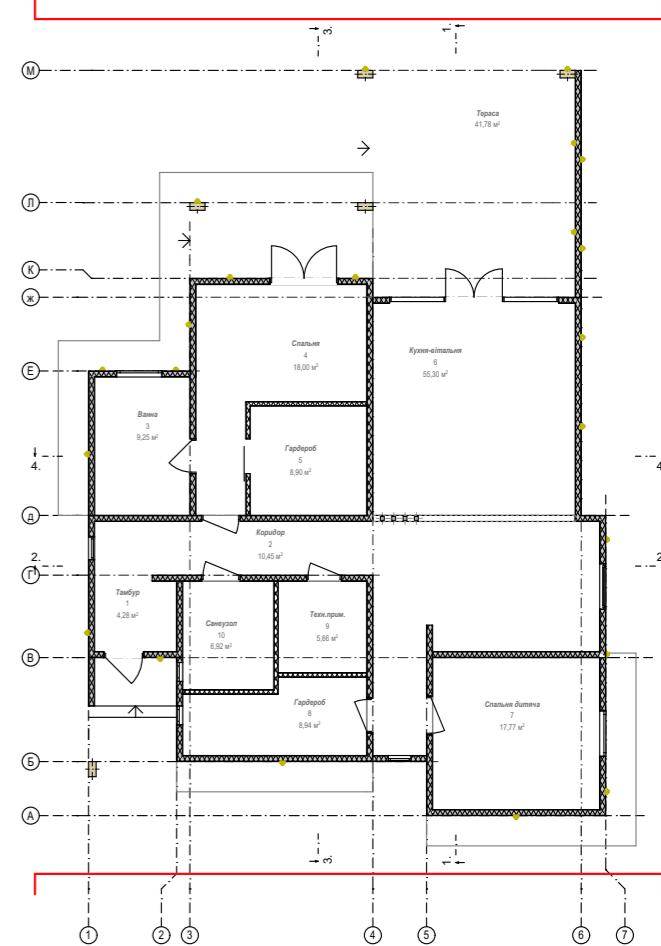


 					Будівництво індивідуального житлового будинку			
Змін.	Кіл.діл	Аркуш	№ Док.	Підпис	Київська обл., Бучанський р-н, с. Віта Поштова	Стадія	Аркуш	Аркушів
ЕП						13		
Виконав					Фасад 1-7, Фасад 7-1 М1:75			
Перевірив					 <b>УКРСІЛБУД</b>			

## Фасад К-А



## Фасад А-К

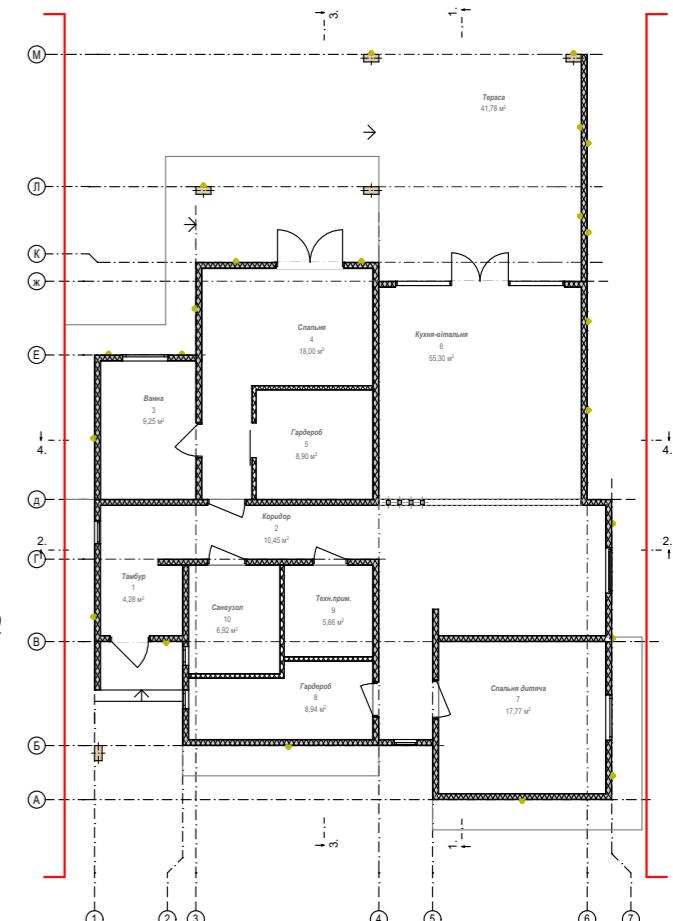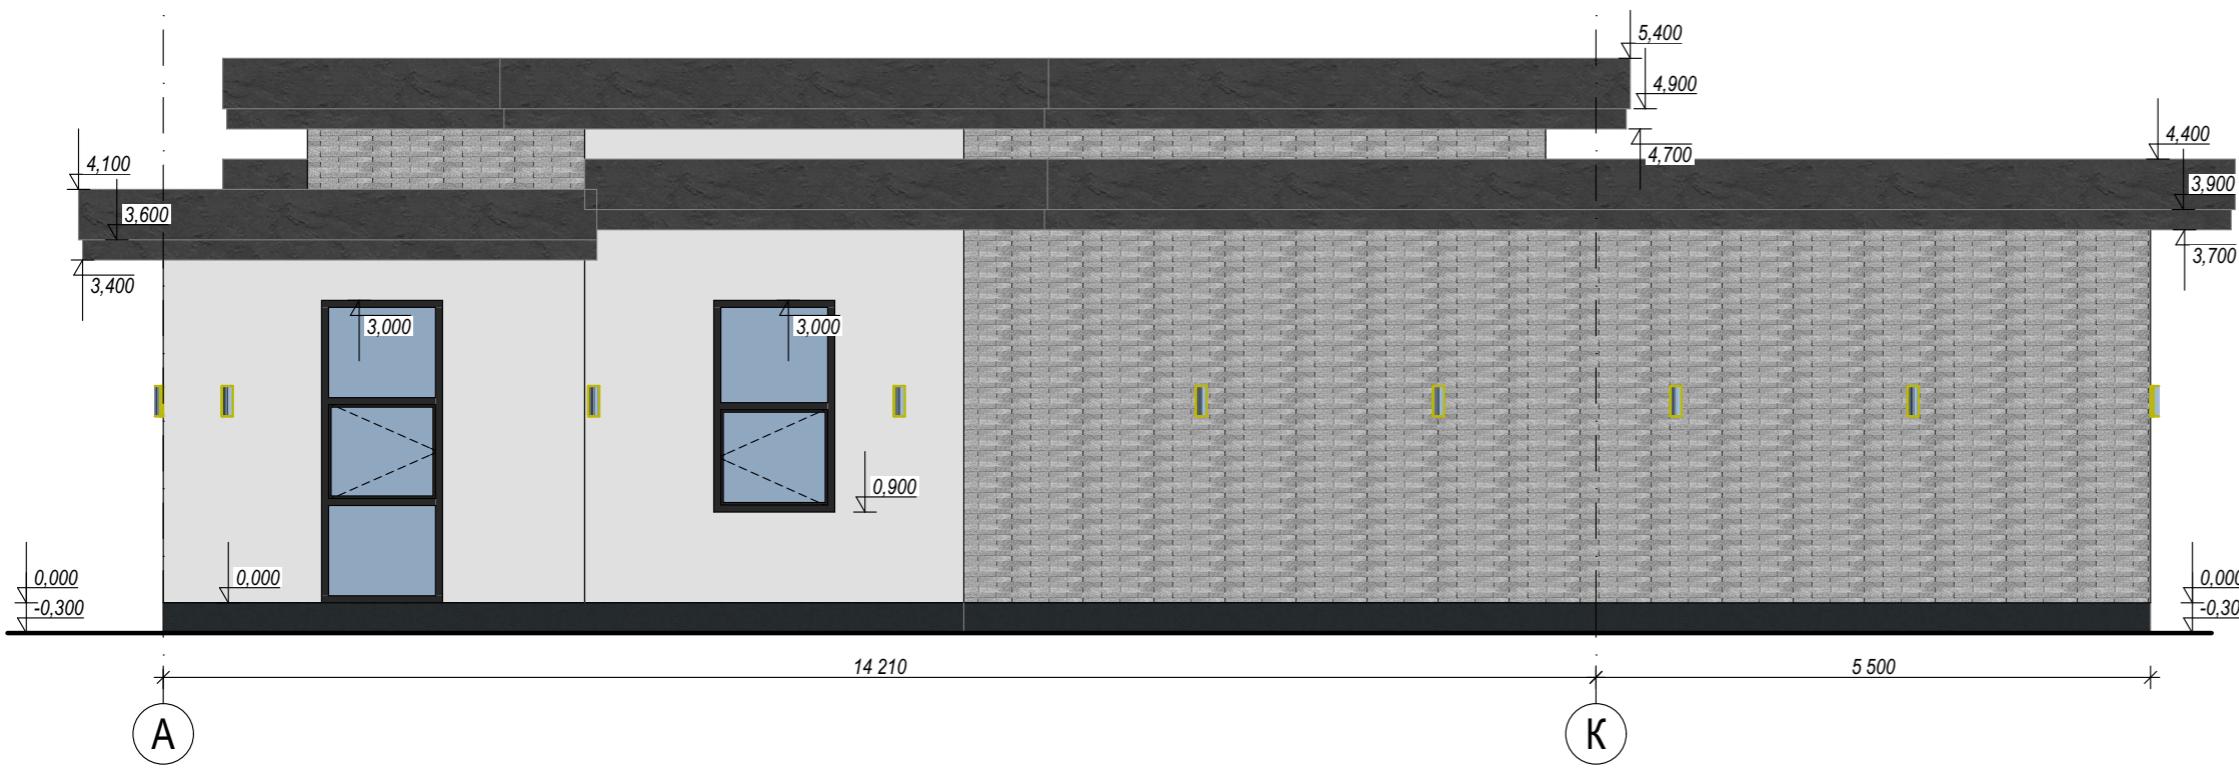

Будівництво індивідуального житлового будинку

Змін. Кіл.діл Аркуш № Док. Підпис  
Київська обл., Бучанський р-н,  
с. Віта Поштова


Стадія Аркуш Аркушів  
ЕП 14

Виконав  
Перевірив

Фасад А-К, Фасад К-А М1:75




### Вузол кріплення стартового бруса до фундаменту

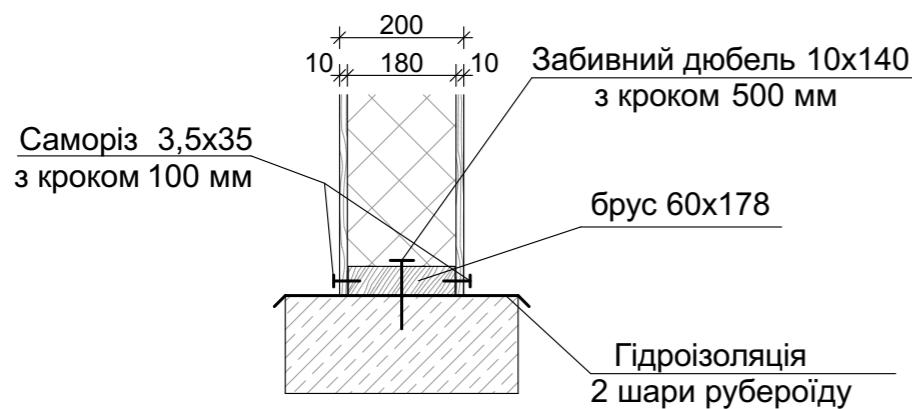


### Вузол з'єднання панелей брусом




### Вузол з'єднання панелей з'єднальною панеллю

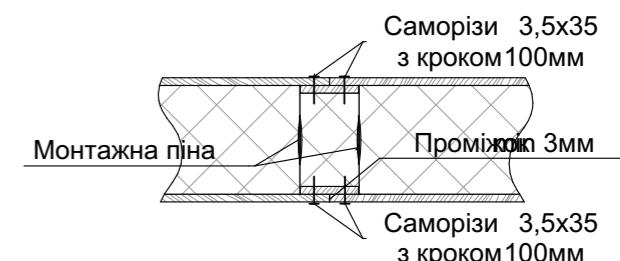


### Т-образний вузол з'єднання панелей 120мм

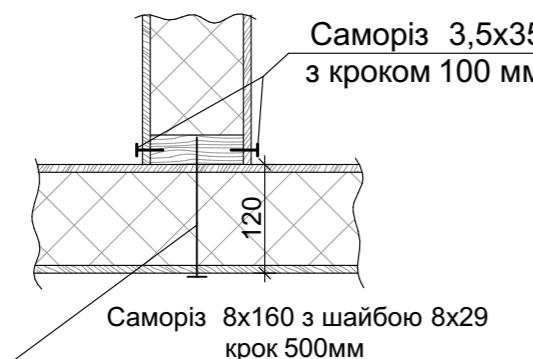


### Т-образний вузол з'єднання панелей 200мм

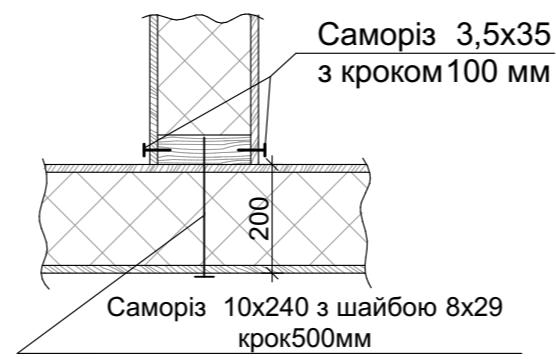

### Т-образний вузол з'єднання панелей

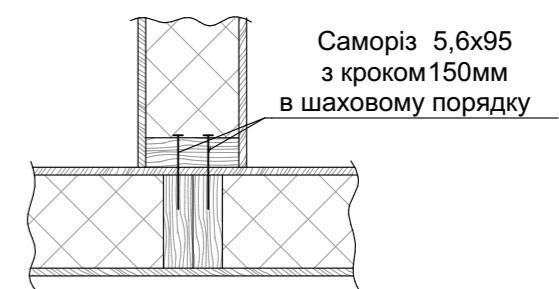

### Кутове з'єднання панелей 200мм

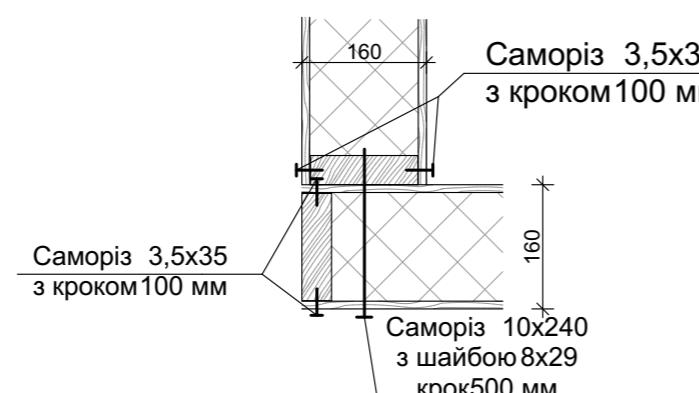

Будівництво індивідуального житлового будинку			
Змін.	Кіл.діл.	Аркуш №	Док.
			Підпис
Виконав			
Перевірив			

Вузли

УкрСпілБуд



				Будівництво індивідуального житлового будинку		
Змін.	Кіл.діл	Аркуш	№ Док.	Підпис	Kиївська обл., Бучанський р-н, с. Віта Поштова	Стадія
					EП	Аркуш
Виконав						Аркушів
Перевірив					Vізуалізація 1	




				Будівництво індивідуального житлового будинку		
				Київська обл., Бучанський р-н, с. Віта Поштова	Стадія	Аркуш
Змін.	Кіл.діл	Аркуш	№ Док.	Підпис	ЕП	Аркуш
Виконав						
Перевірив						
				Візуалізація 2		



				Будівництво індивідуального житлового будинку		
Змін.	Кіл.діл.	Аркуш	№ Док.	Підпис	Kиївська обл., Бучанський р-н, с. Віта Поштова	Стадія
						Аркуш
Виконав						Аркуш
Перевірив					Vізуалізація 3	18

  
**УкрСпБуд**

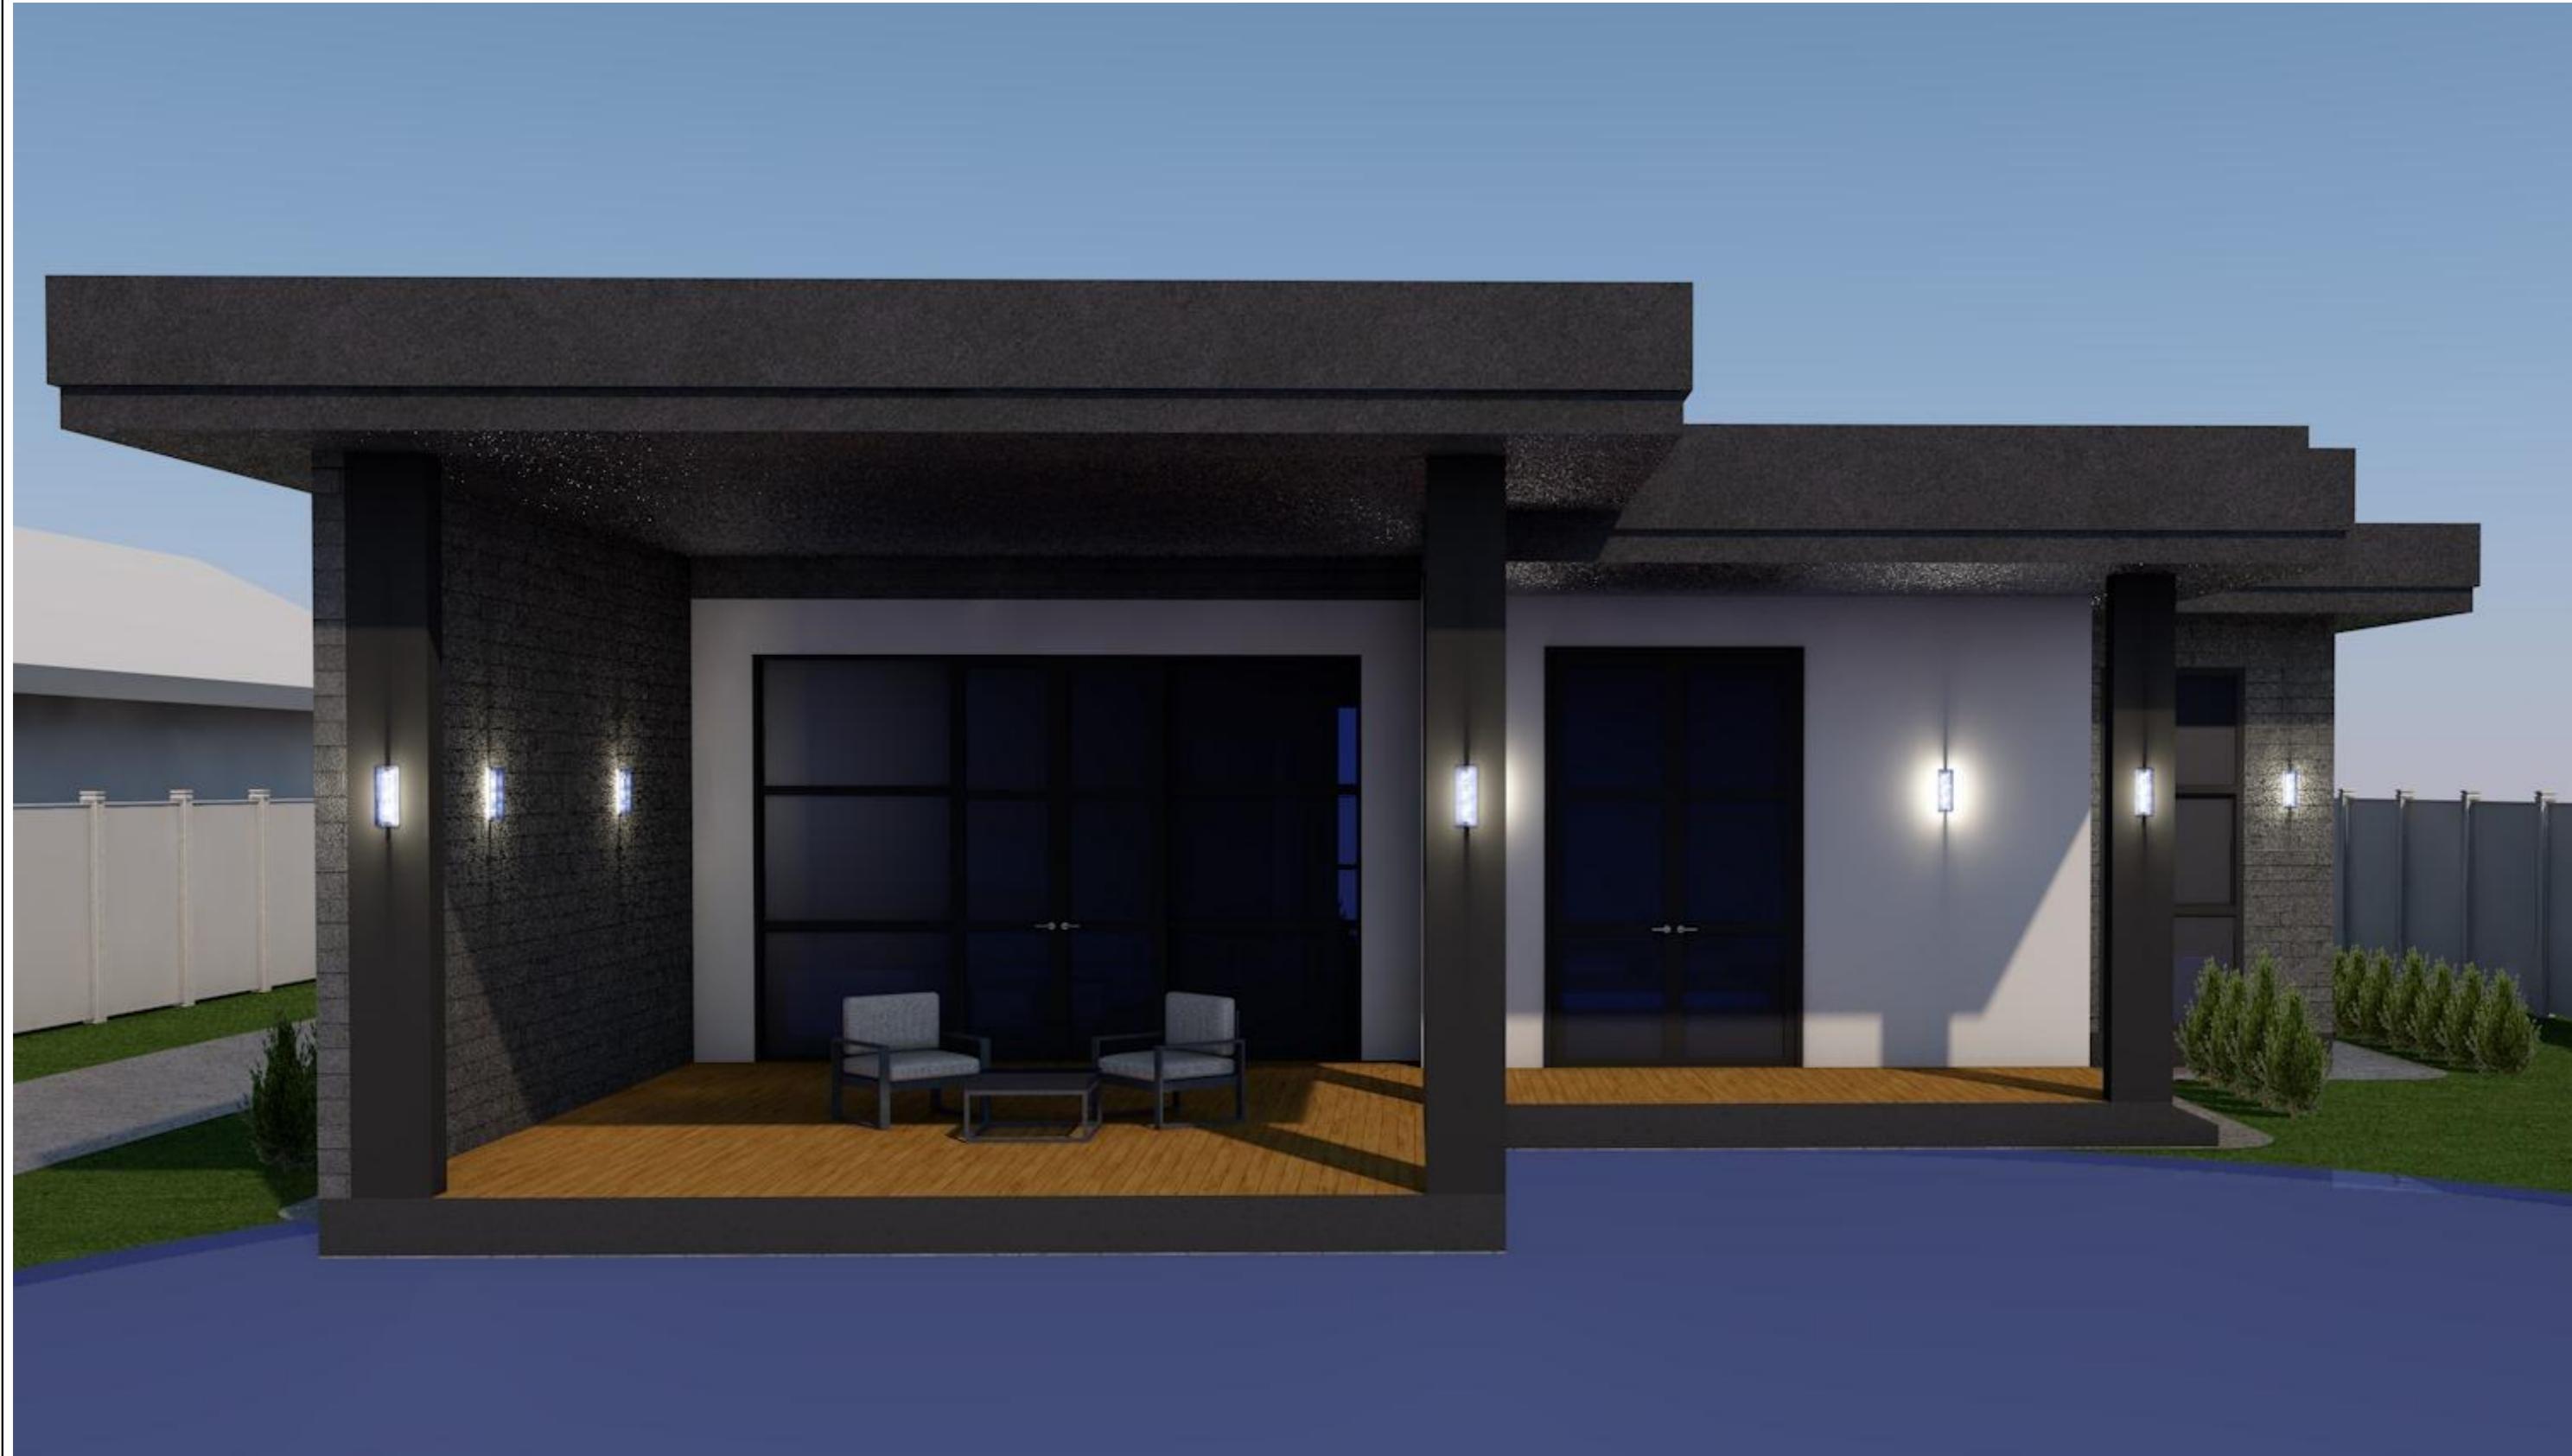

				Будівництво індивідуального житлового будинку		
Змін.	Кіл.діл.	Аркуш	№ Док.	Підпис	Kиївська обл., Бучанський р-н, с. Віта Поштова	Стадія
					EП	Аркуш
Виконав						Аркуш
Перевірив						19
					Vізуалізація 4	
						 <b>УкрСіпБуд</b>



					Будівництво індивідуального житлового будинку			
					Kиївська обл., Бучанський р-н, с. Віта Пощтова	Стадія	Аркуш	Аркушів
Змін.	Кіл.діл	Аркуш	№ Док.	Підпис		ЕП	20	
Виконав								
Перевірив						Візуалізація 5		